

BIMCO STUDIO BARCELONA

BARCELONA, SPAIN • OFFICIAL ARCHITECTURAL MONOGRAPH • EDITION 2026



BIMCO

VOLUME II: RESIDENTIAL APARTMENTS & ADVANCED FACADES

BUILDING ENVELOPE TECTONICS & URBAN COLLECTIVE FORM

Comprehensive monographs of multi-family dwellings and facade engineering in uninterrupted project continuity

COLLABORATIVE ARCHITECTURAL PRACTICE & BIM DIRECTION

SOHEIL MASTI

BIM Director & Computational Architect

Information Architecture & LOD 350 Audit

SIAVASH PAZOOKI

Senior Architectural Designer & Visualizer

M.Arch & Lead Concept Formulator

THE ARCHITECTURE OF URBAN SKINS & COLLECTIVE HOUSING

Tectonic Depth, Material Permanence, and Solar Modulation

The facade is the public face of architecture—the mediator between the urban realm and private human dwelling. At BIMCO Studio Barcelona, we treat the building skin as a high-performance tectonic system that balances light, privacy, acoustic buffering, and energy conservation.

Our residential projects—from terraced mountain dwellings in Dalkhani to mid-rise luxury enclaves in Darrous and high-density modular towers—demonstrate rigorous structural logic.

Every joint, reveal, and stone anchor is coordinated in BIM to bridge the gap between bold aesthetic visions and flawless on-site installation.

UNINTERRUPTED MONOGRAPH PROTOCOL

Every project is presented with complete continuity from plans to execution.

PROJECT ARCHIVE & SEQUENCE

Chronological Architectural Records (All Sheets in Consecutive Order)

01

DARROUS RESIDENTIAL FACADE 2020

Complete Project Presentation (6 Consecutive Sheets)

PGS 03 - 08 / 22

02

DALKHANI RESIDENTIAL TERRACES

Complete Project Presentation (5 Consecutive Sheets)

PGS 09 - 13 / 22

03

URBAN MID-RISE & MONUMENTAL PALACE

Complete Facade Typologies (7 Consecutive Sheets)

PGS 14 - 20 / 22

04

PRACTICE LEADERSHIP & ARCHITECTS

Soheil Masti & Siavash Pazooki Credentials

PAGE 21 / 22

05

BIMCO VERIFICATION ARCHIVE

Technical Standards & Quality Assurance Protocols

PAGE 22 / 22





An elevation drawing is an orthographic projection drawing that shows one side of the house. The purpose of an elevation drawing is to show the finished appearance of a given side of the house and furnish vertical height dimensions. Four elevations are customarily drawn, one for each side of the house.





A front elevation design is basically a part of a scenic design which highlights the scenic element or the entire set as seen from the front view with or without measurements. Most of the front elevation designs show the measurements to get a better understanding of the building so that it can be drafted or quickly drawn by an architect. The front elevation of a home plan is a straight-on view of the house as if you were looking at it from a perfectly centered spot on the same plane as the house.

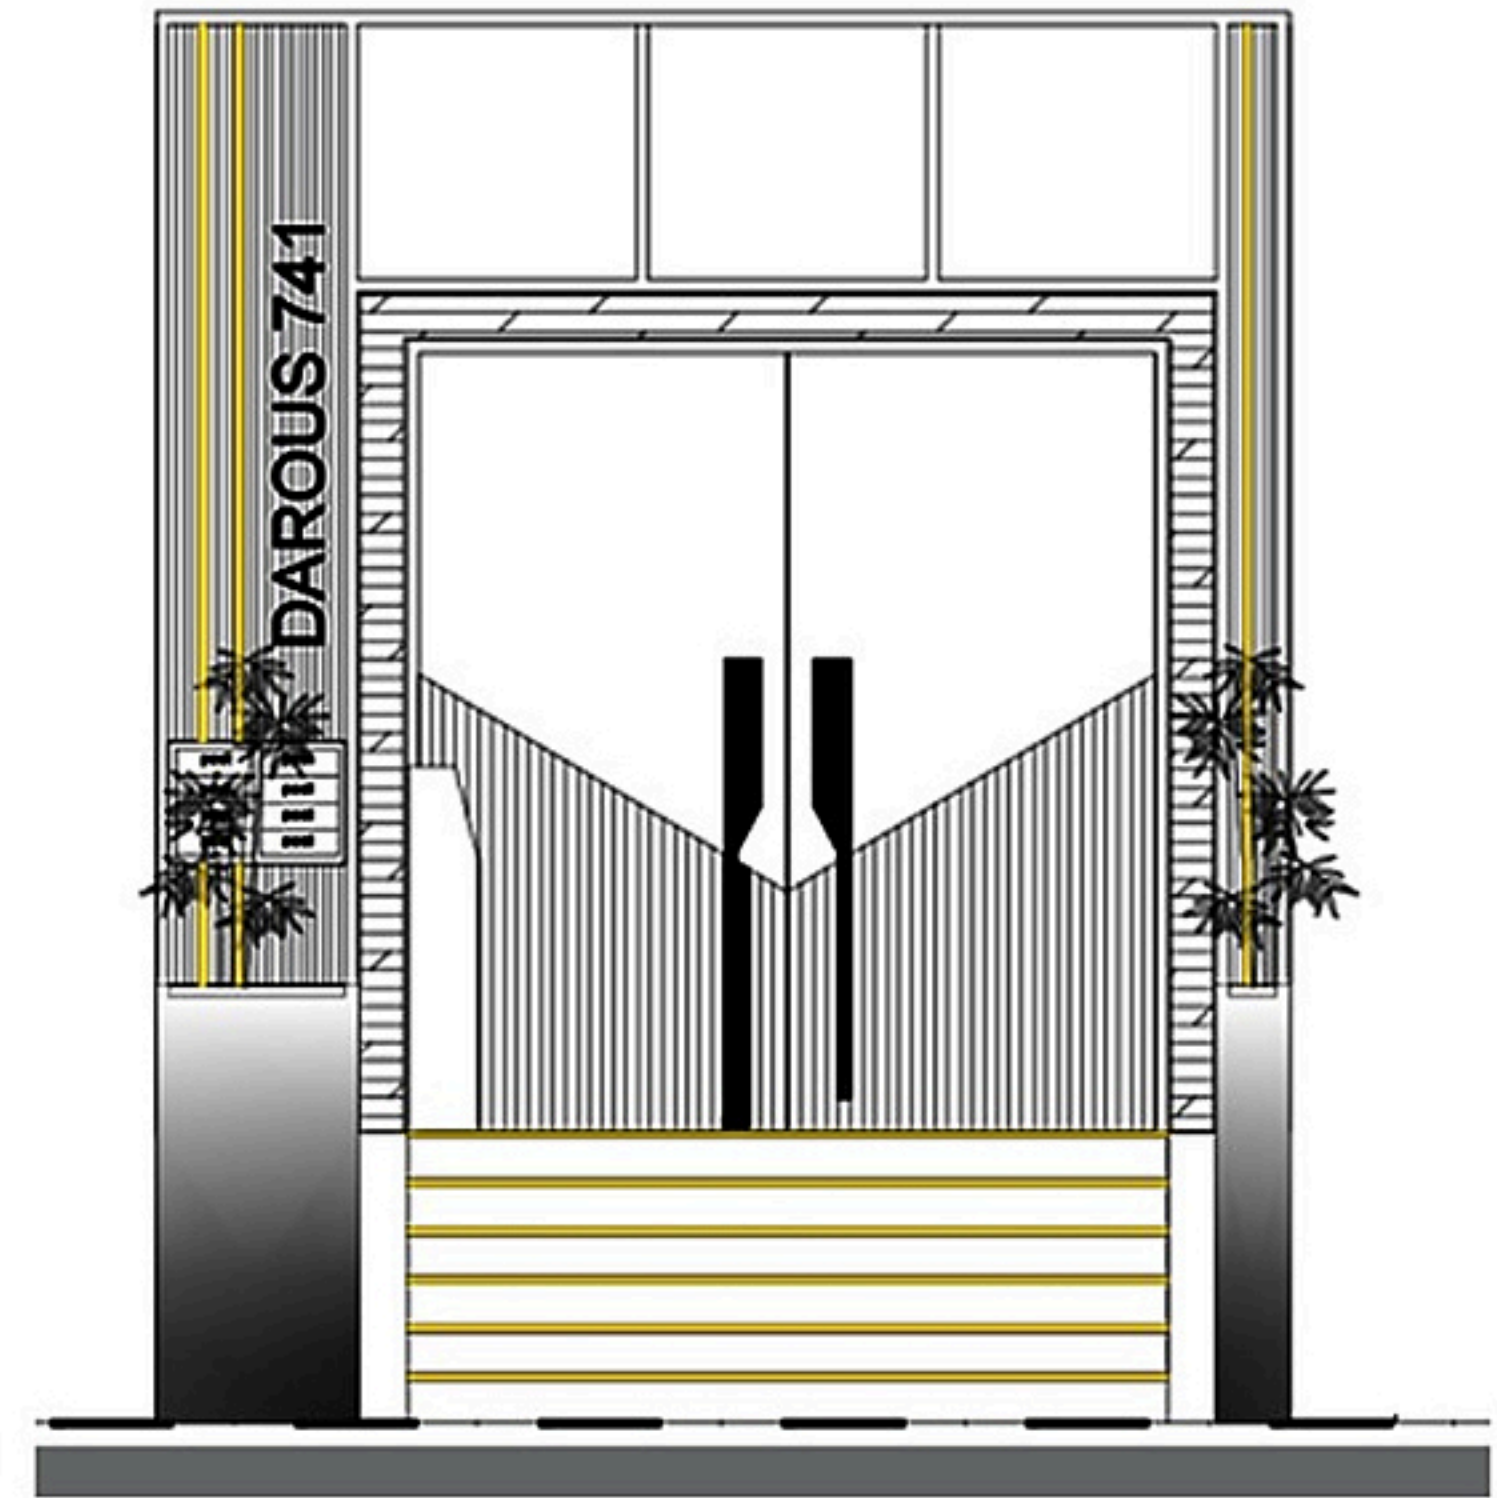

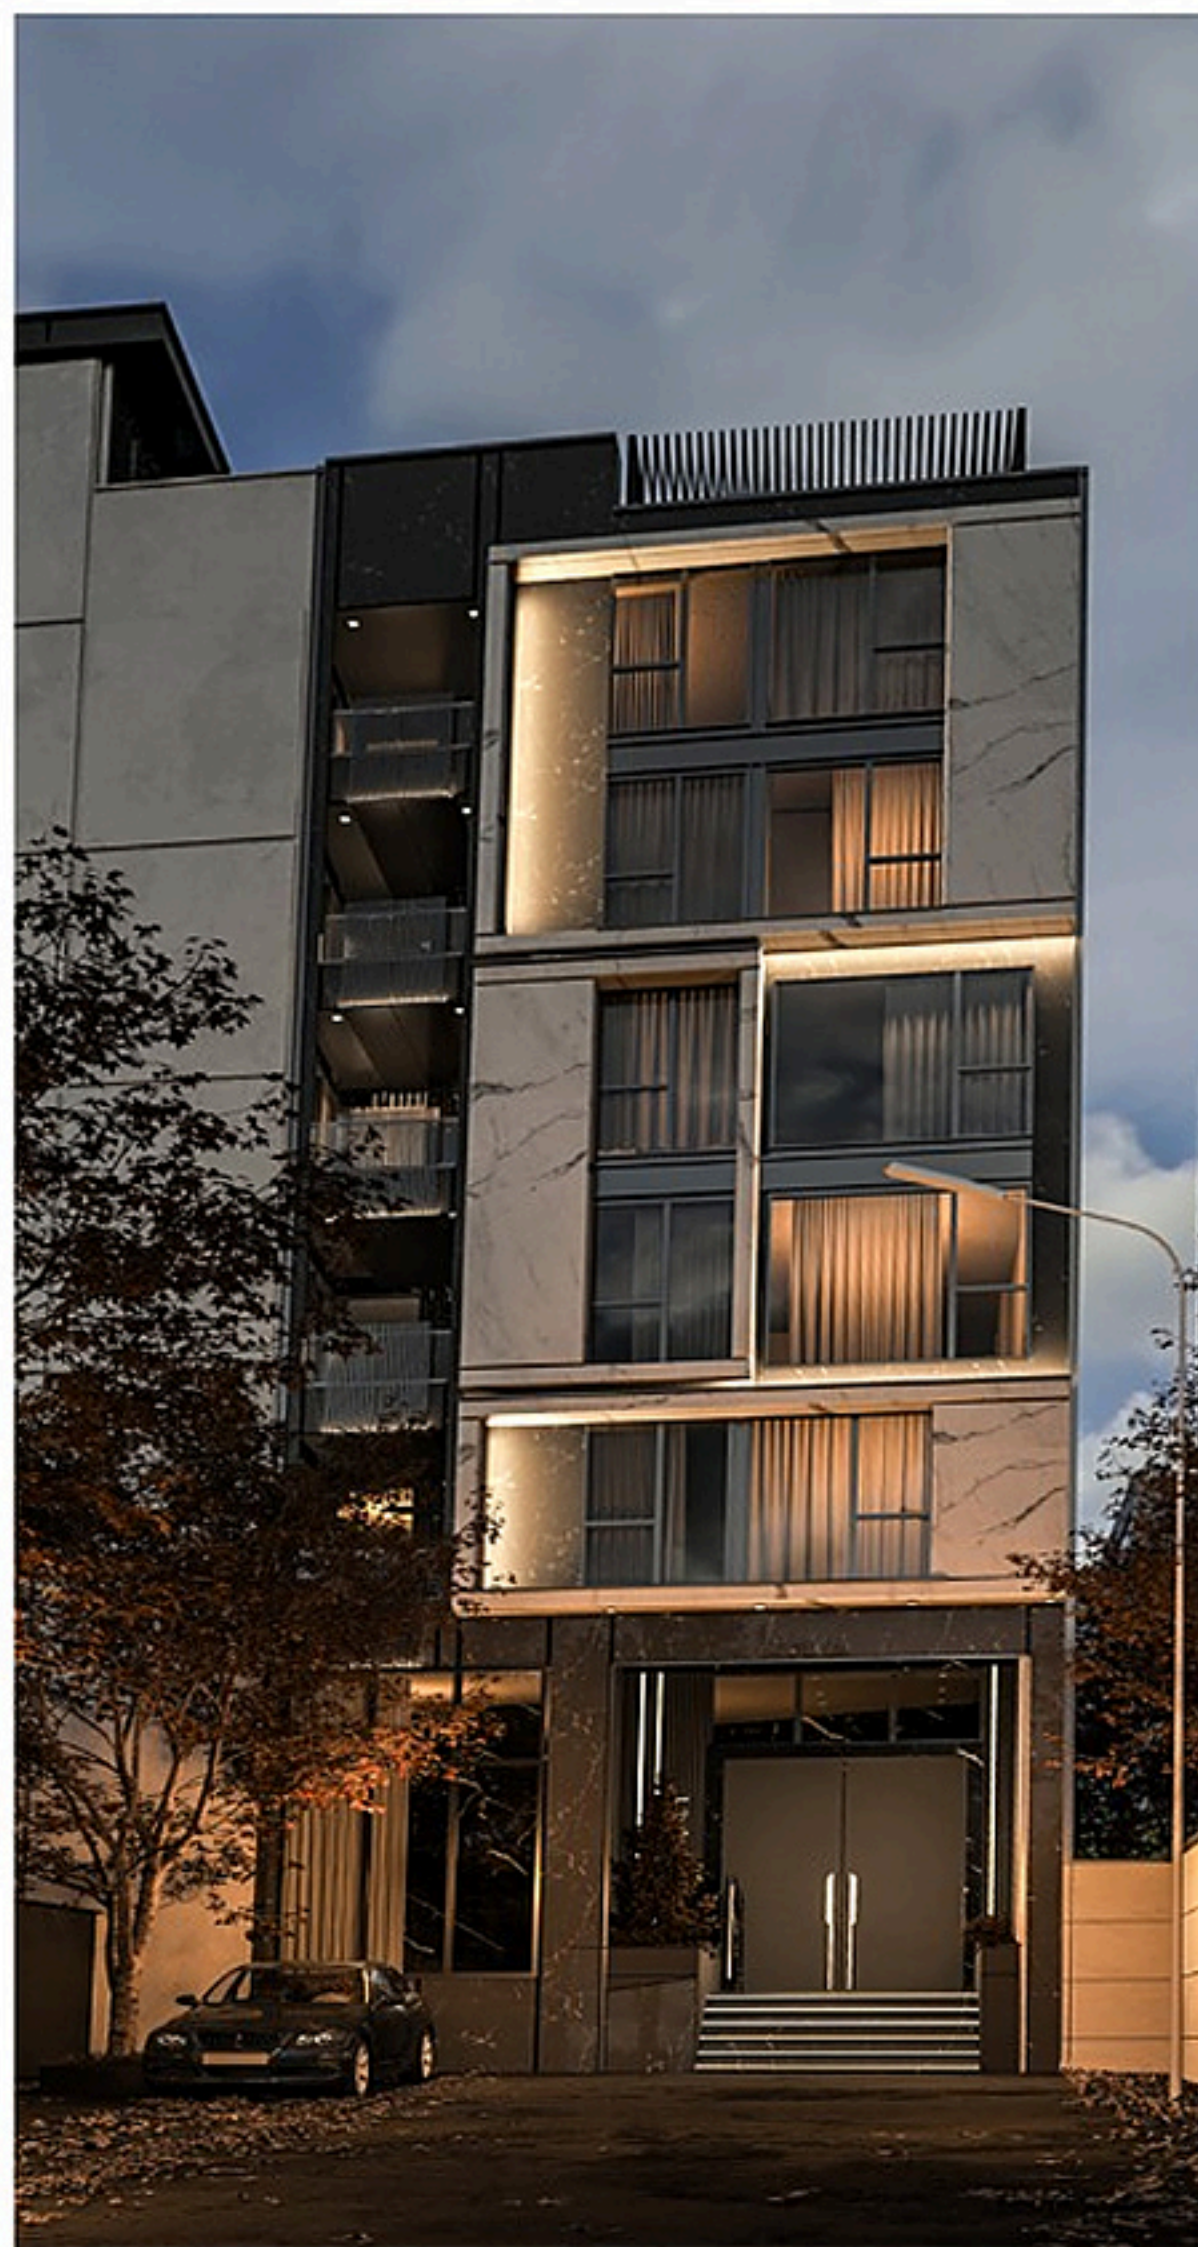

Modern house elevations are distinguished by several defining features



Minimalism: Modern designs often emphasize a minimalist approach, characterized by clean, uncluttered lines and a lack of ornamental detailing

Large Windows: Expansive windows are a hallmark of modern elevations, allowing for ample natural light and a seamless connection between the indoors and outdoors

Innovative Materials: The use of innovative materials such as glass, steel, and concrete is common, offering both aesthetic appeal and functional benefits

Geometric Forms: Modern elevations frequently incorporate bold geometric forms and asymmetrical compositions, making strong architectural statements

Integration with Nature: Many modern designs focus on harmonizing the building with its natural surroundings, often using elevation to enhance this connection

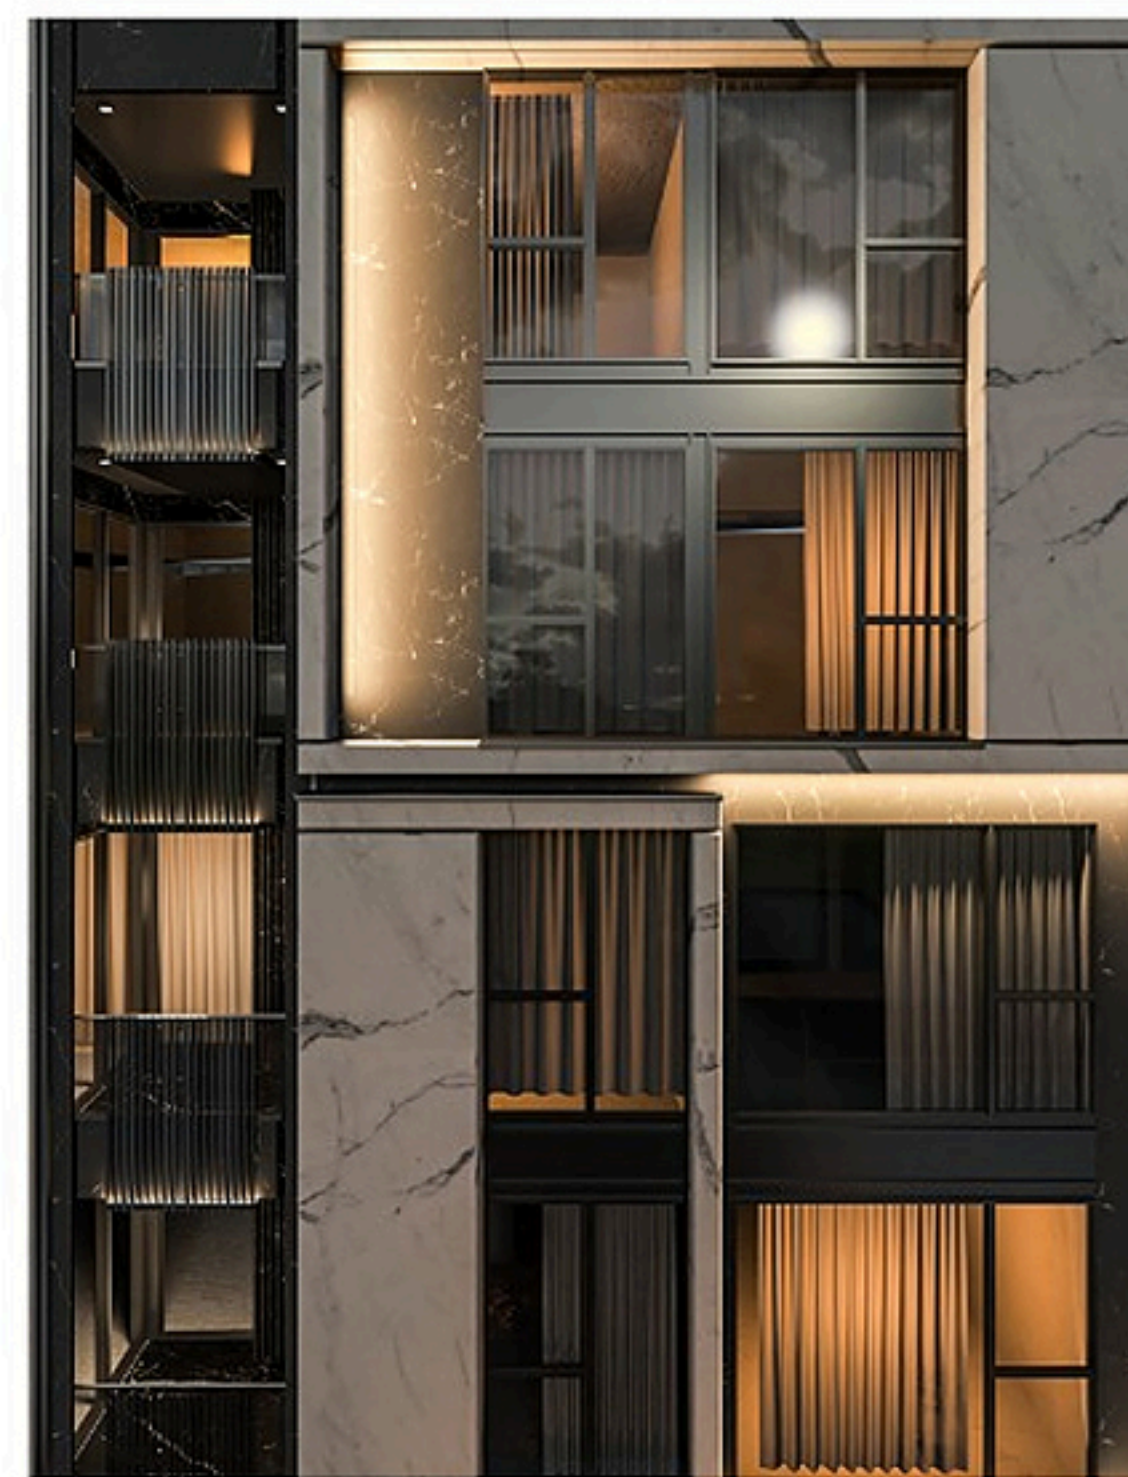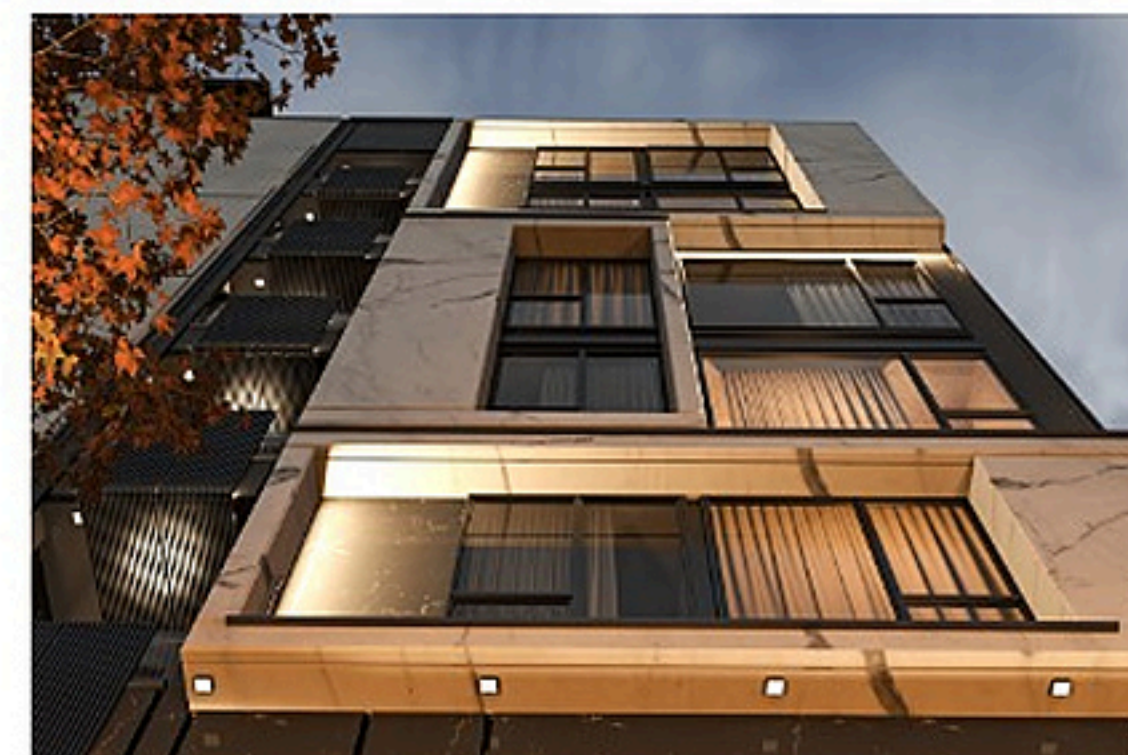



Modern house elevation refers to the external design and architectural elements of a house's front façade. It plays a crucial role in defining the aesthetic appeal and character of a modern home. In contemporary architecture, house elevation is not just about creating a visually appealing structure; it's about blending form with functionality, innovation with sustainability, and design with the surrounding environment.





Interior elevations are very important to the owner and the builder. Interior elevations are usually drawn for cabinets and special built-in fixtures. They normally show everything that will be located on the finished wall. The set of construction drawing includes interior elevations of the teller's counter. These elevations are drawn in conjunction with the floor plan so that all dimensions for constructing the cabinets are shown on one of the two drawings.





An elevation drawing is an orthographic projection drawing that shows one side of the house. The purpose of an elevation drawing is to show the finished appearance of a given side of the house and furnish vertical height dimensions. Four elevations are customarily drawn, one for each side of the house.


As a drawing, an elevation is a two-dimensional projection perpendicular to the vertical plane – meaning, it is a flat view seen while the “observer” is looking forward. Most commonly, elevations portray the individual sides of a house.

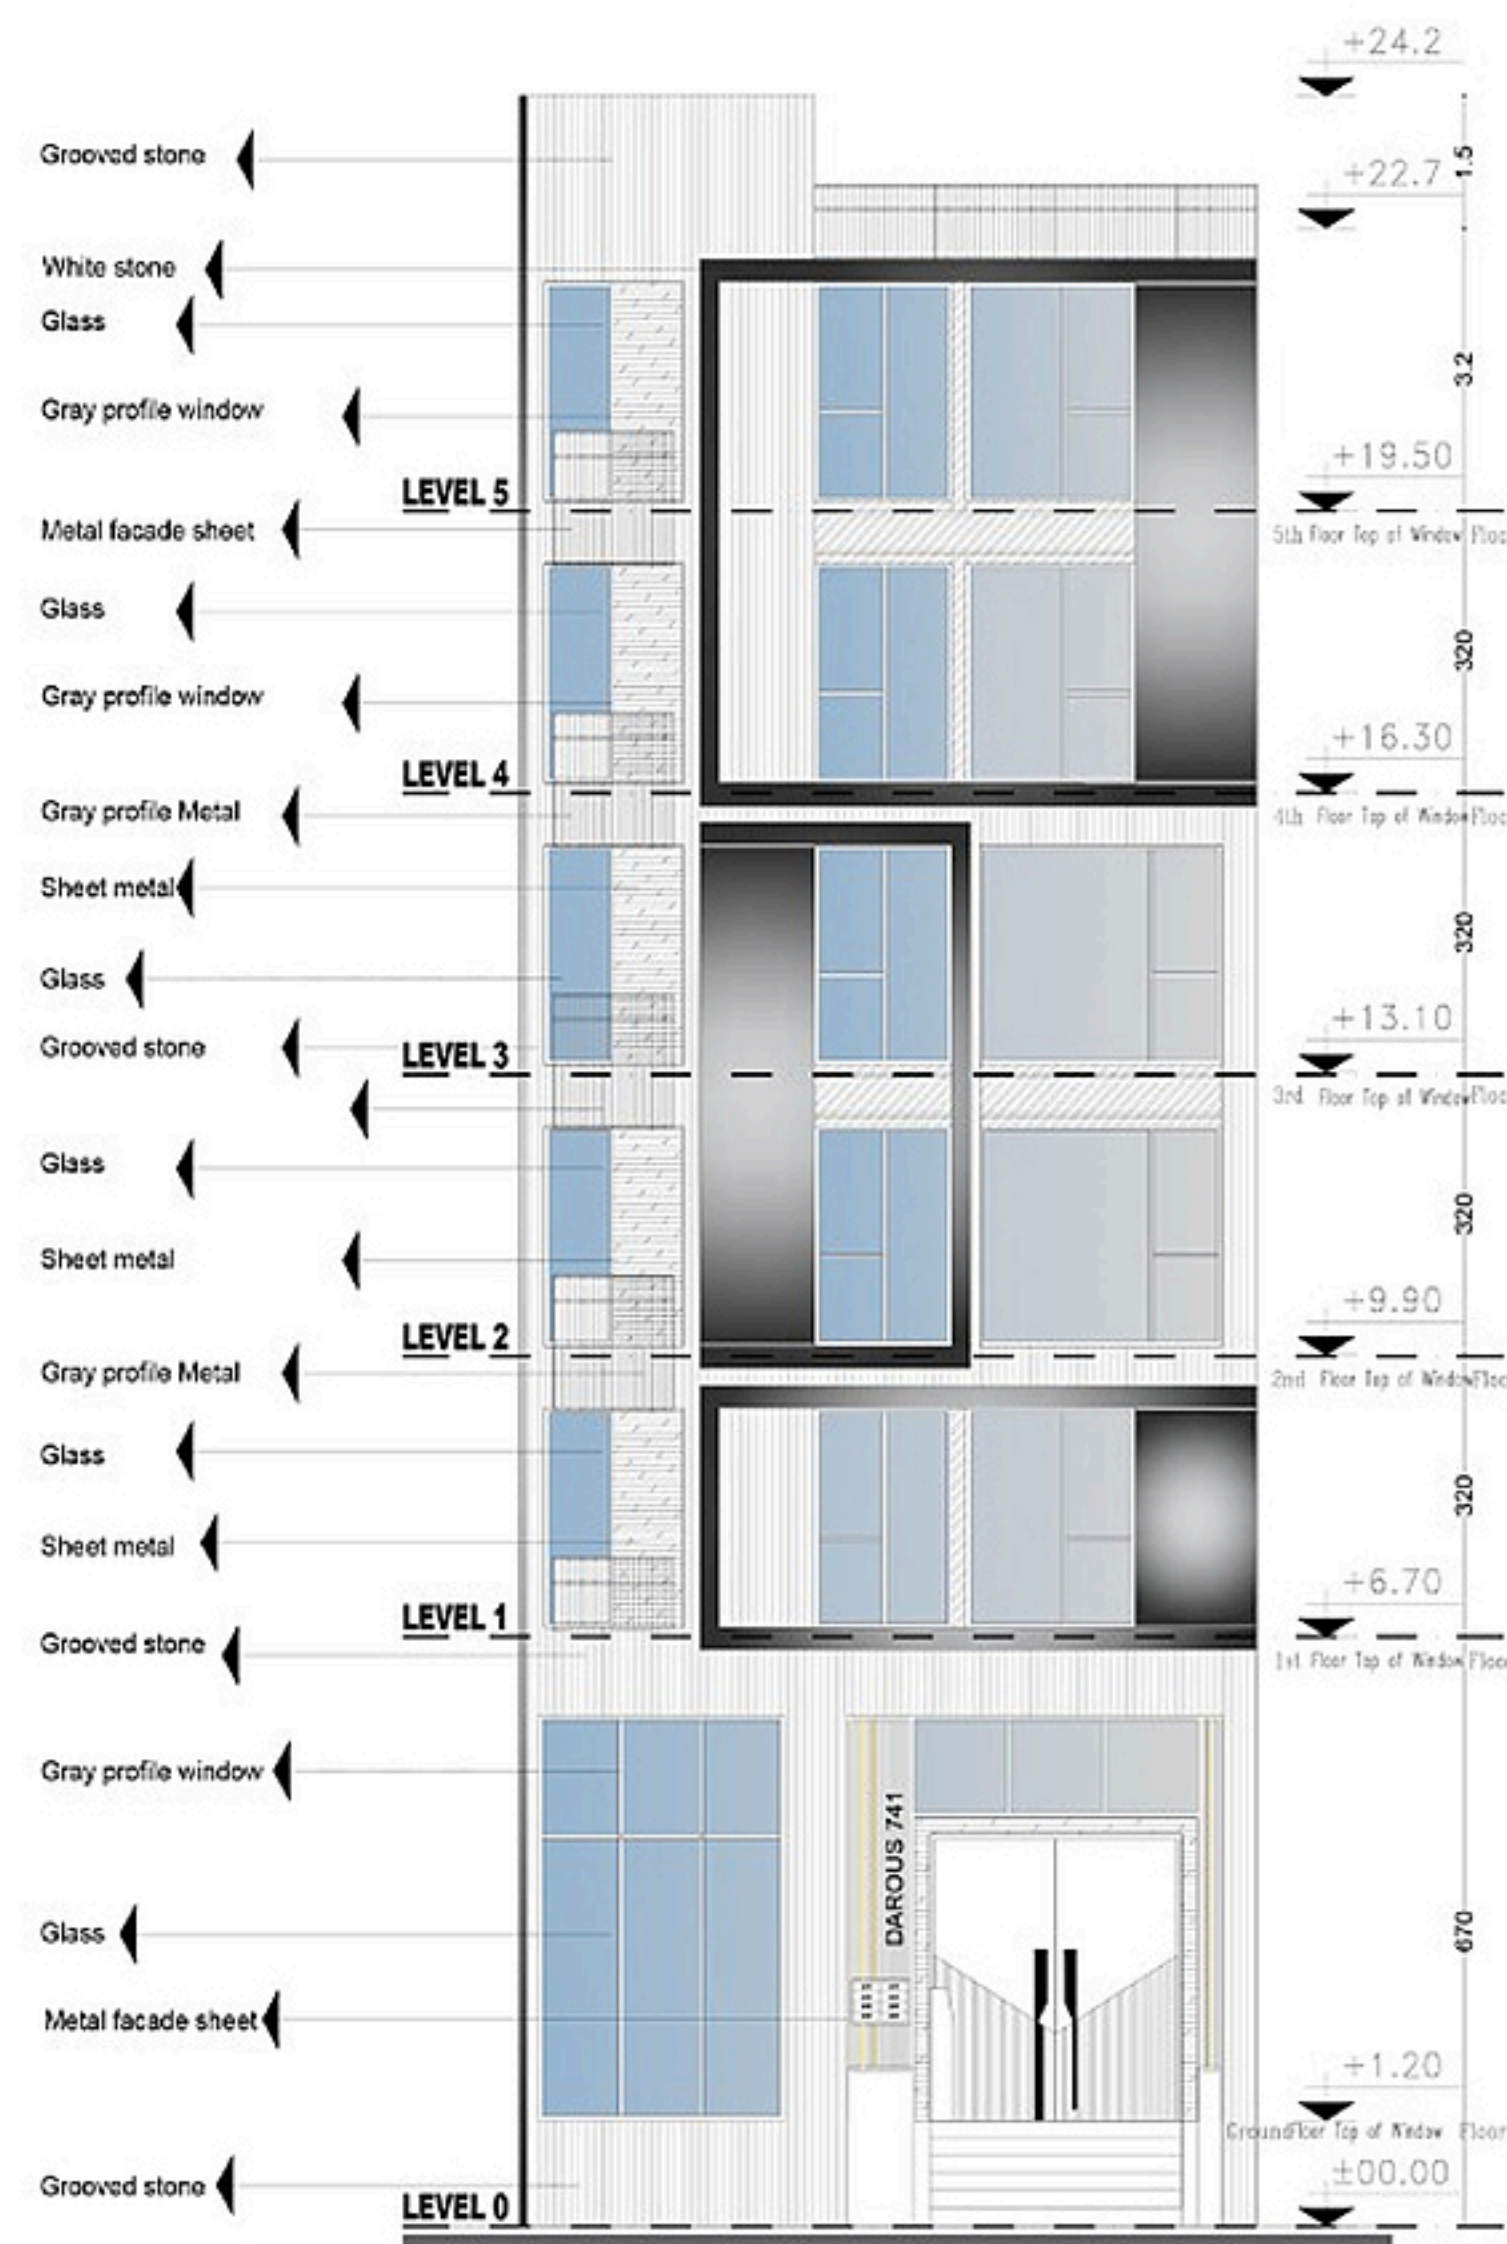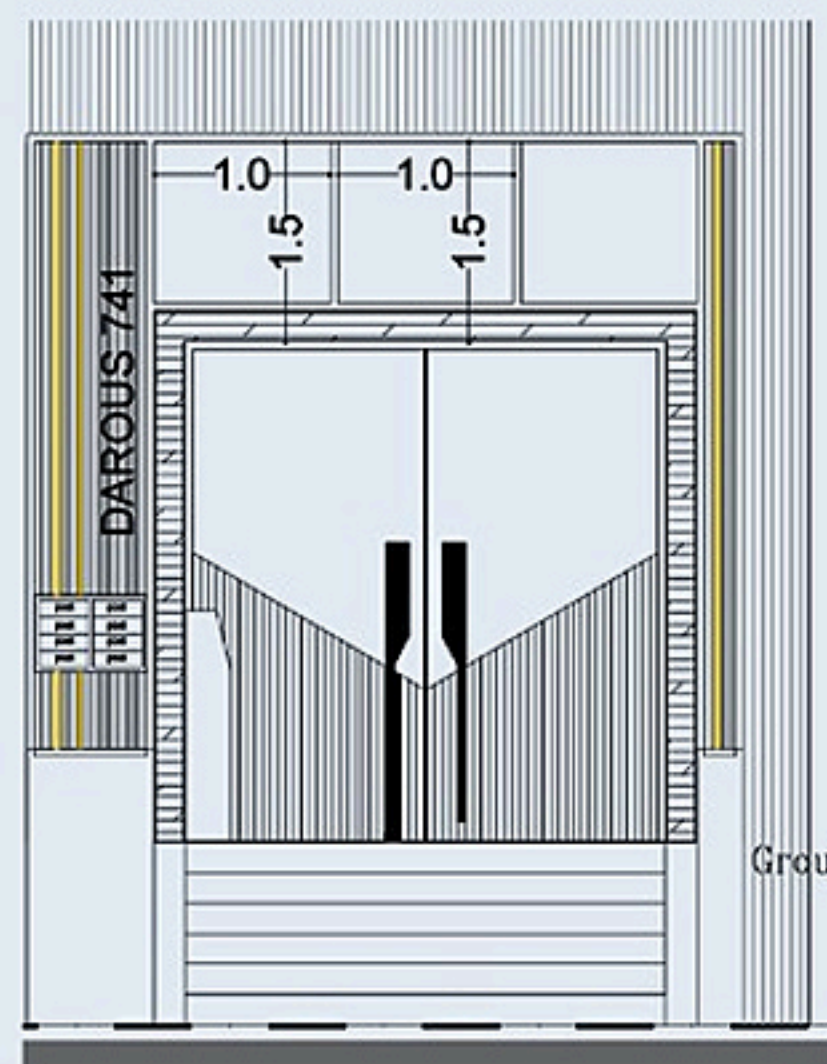

The word facade originally comes from the Italian word "facciata", and is defined as the outside or all of the external faces of a building. The term is frequently used to refer just to the main or front face of a house.

Along with the roof, it is one of the most important elements of a building, since it acts as the primary barrier against external weather elements that could damage the health of the structure, such as rain, snow, wind, frosts, sun, etc.

301	---	White stone	
302	---	Mixed facade stone	
303	---	Black stone	
304	---	Ground stone	
305	---	Great metal	
306	---	Glass	

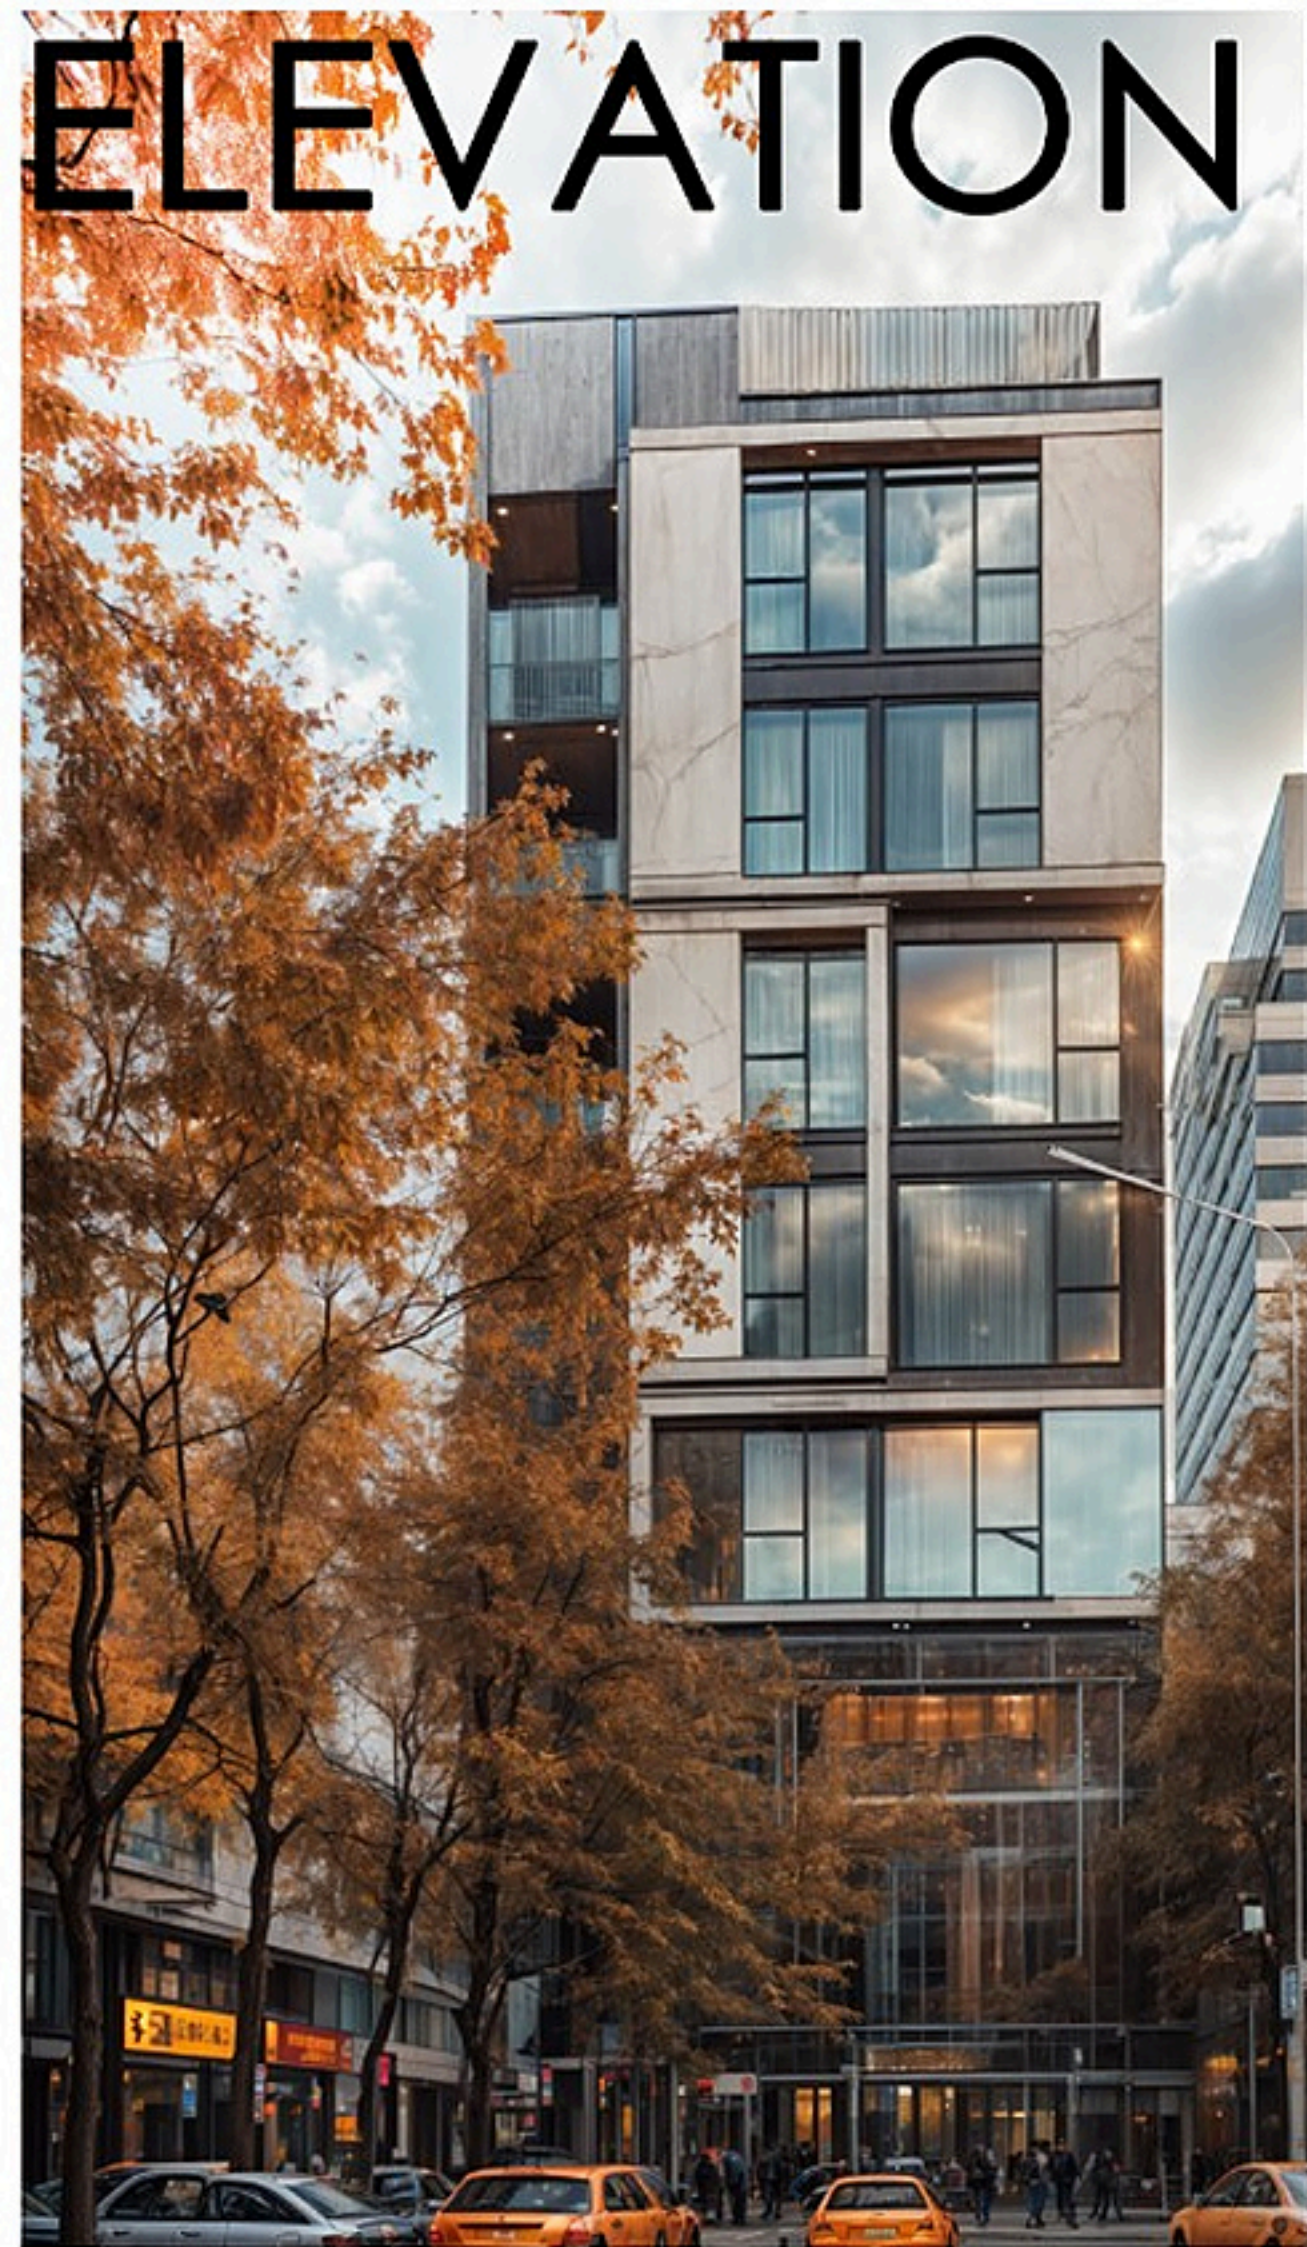

ELEVATION DESIGN

CLIENT : MR GHORBANY
PLACE :DAROOS
YEAR: 2020


Modern elevation design emphasizes clean lines, minimalist aesthetics, and a focus on functionality, often incorporating large windows, flat roofs, and a blend of materials like glass, stone. It prioritizes open spaces, natural light, and seamless integration with the surrounding environment, creating a sleek, contemporary look.




RESIDENTIAL DALKHANI PROJECT






Residential mountain homes often blend rustic charm with modern comforts, featuring natural materials like wood and stone, large windows for scenic views, and functional layouts designed for mountain living

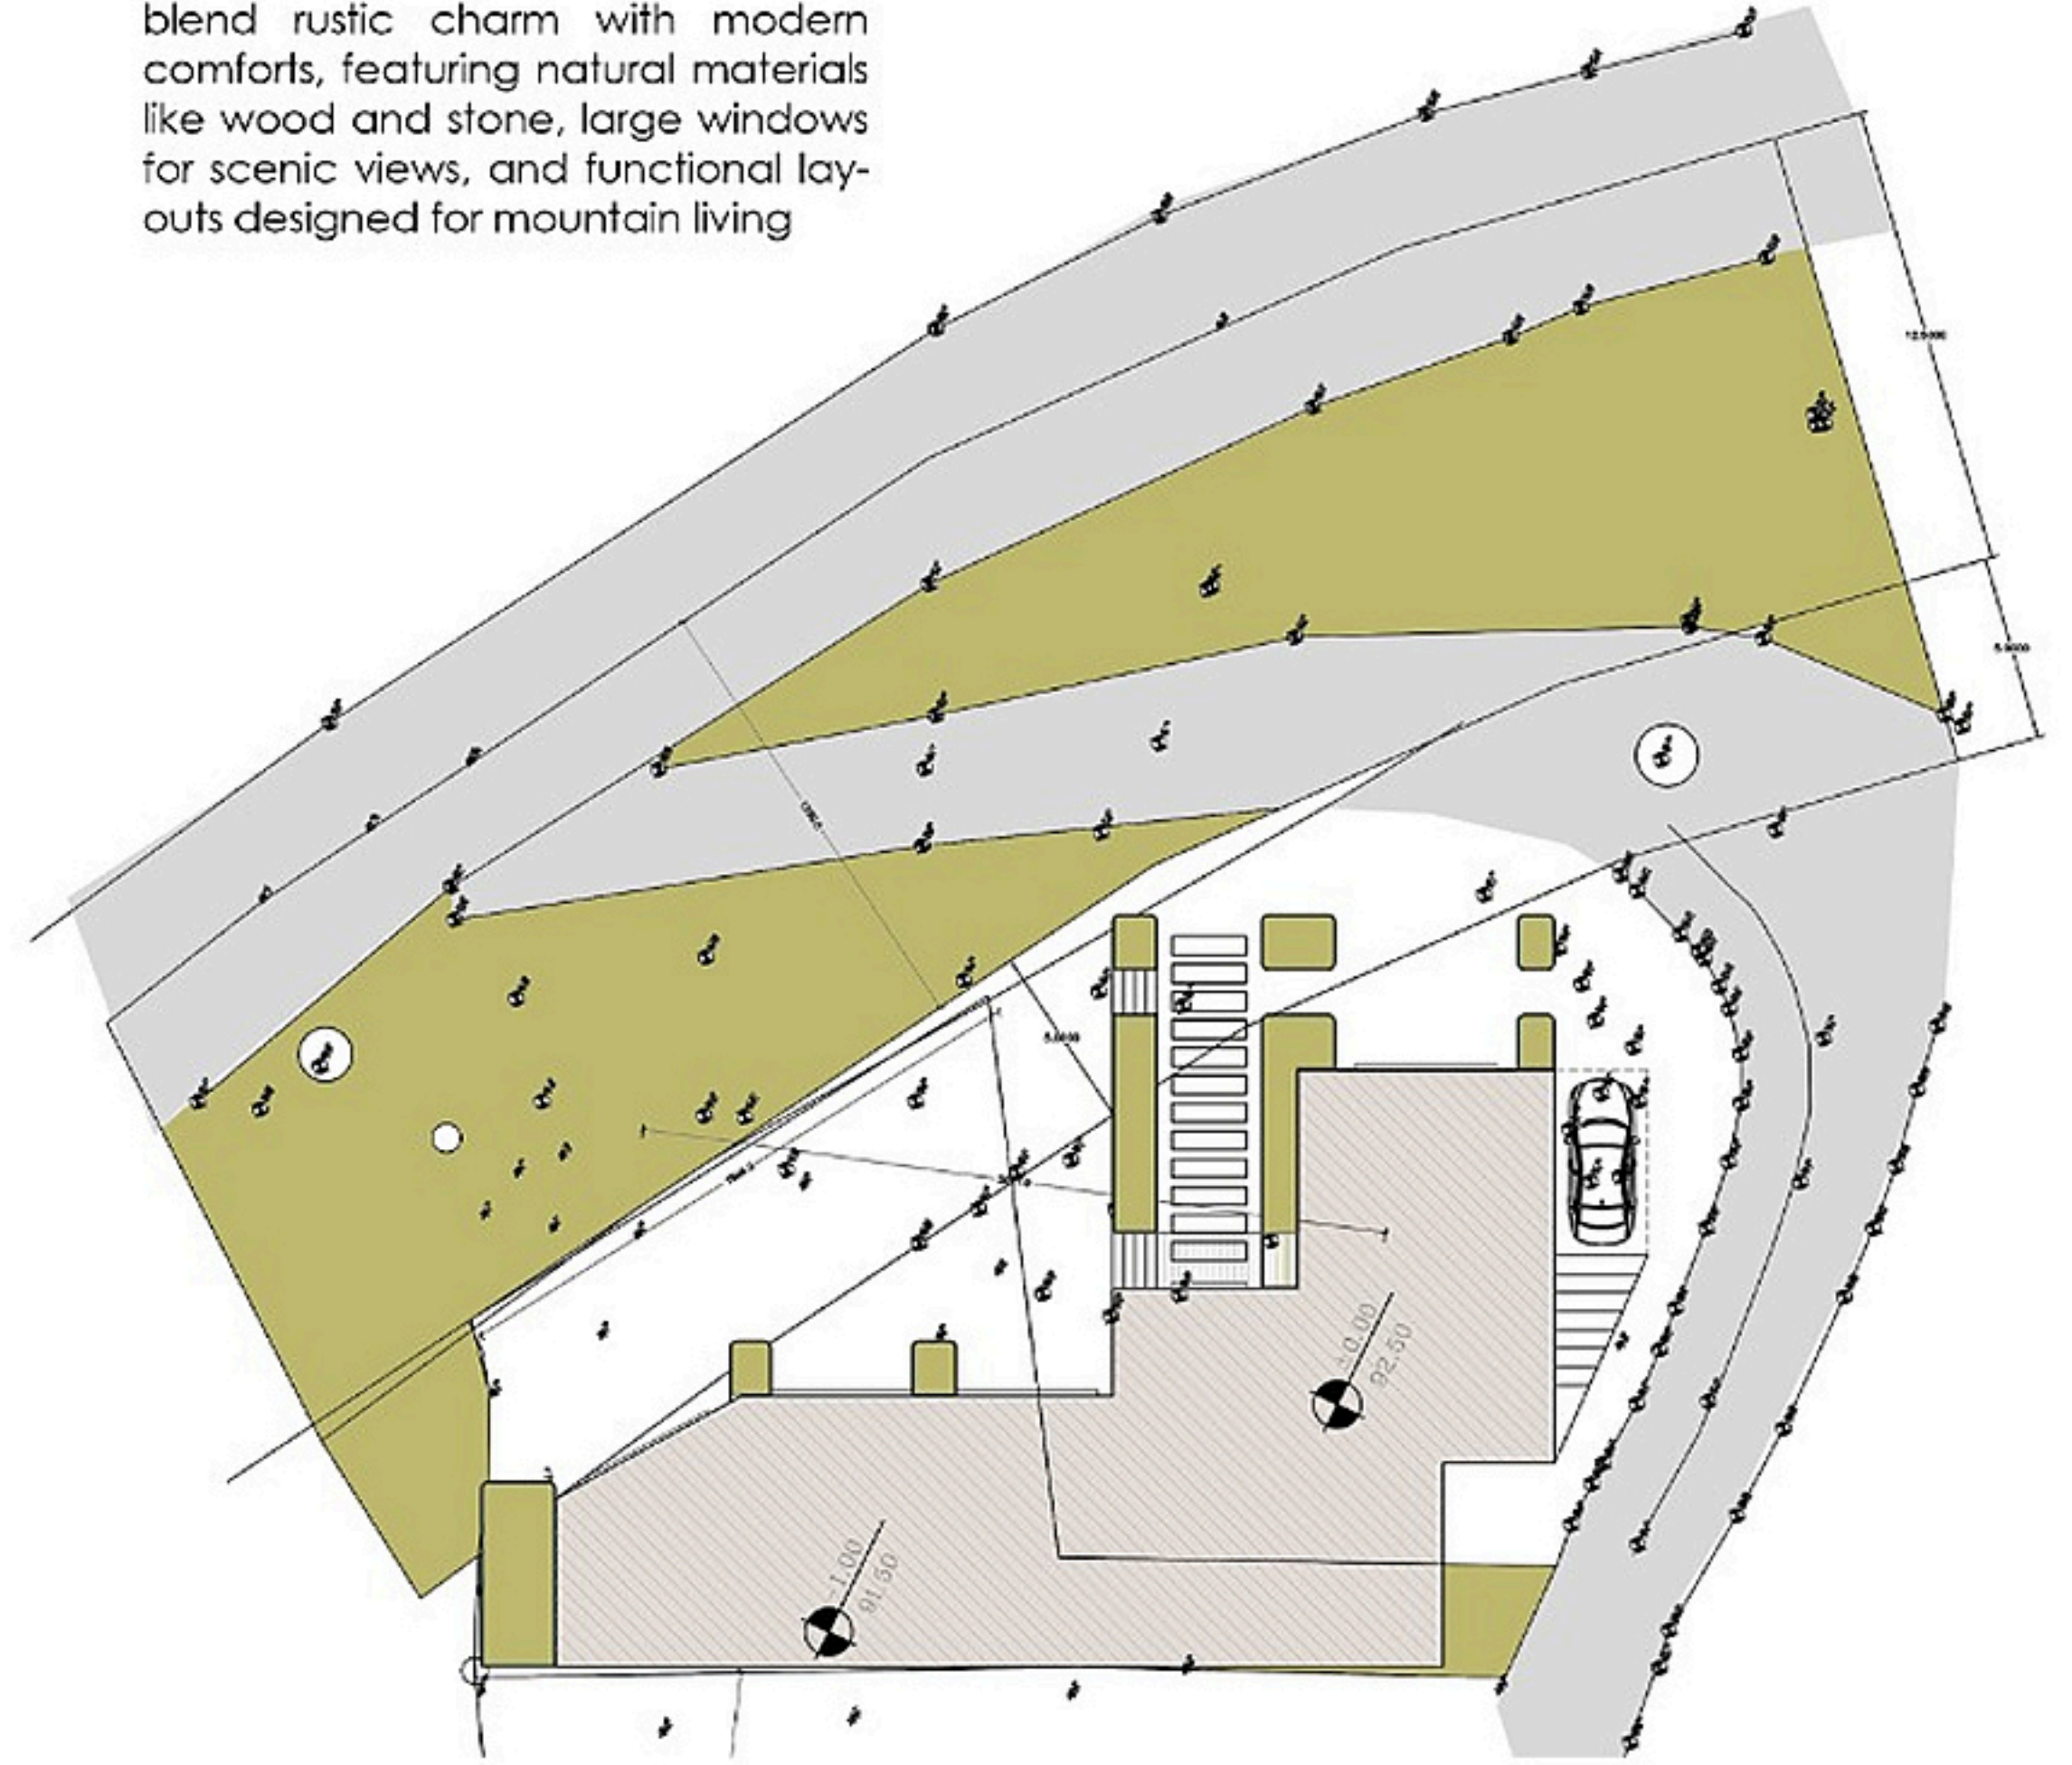

محل قرار گیری ساختمان در سایت پلان

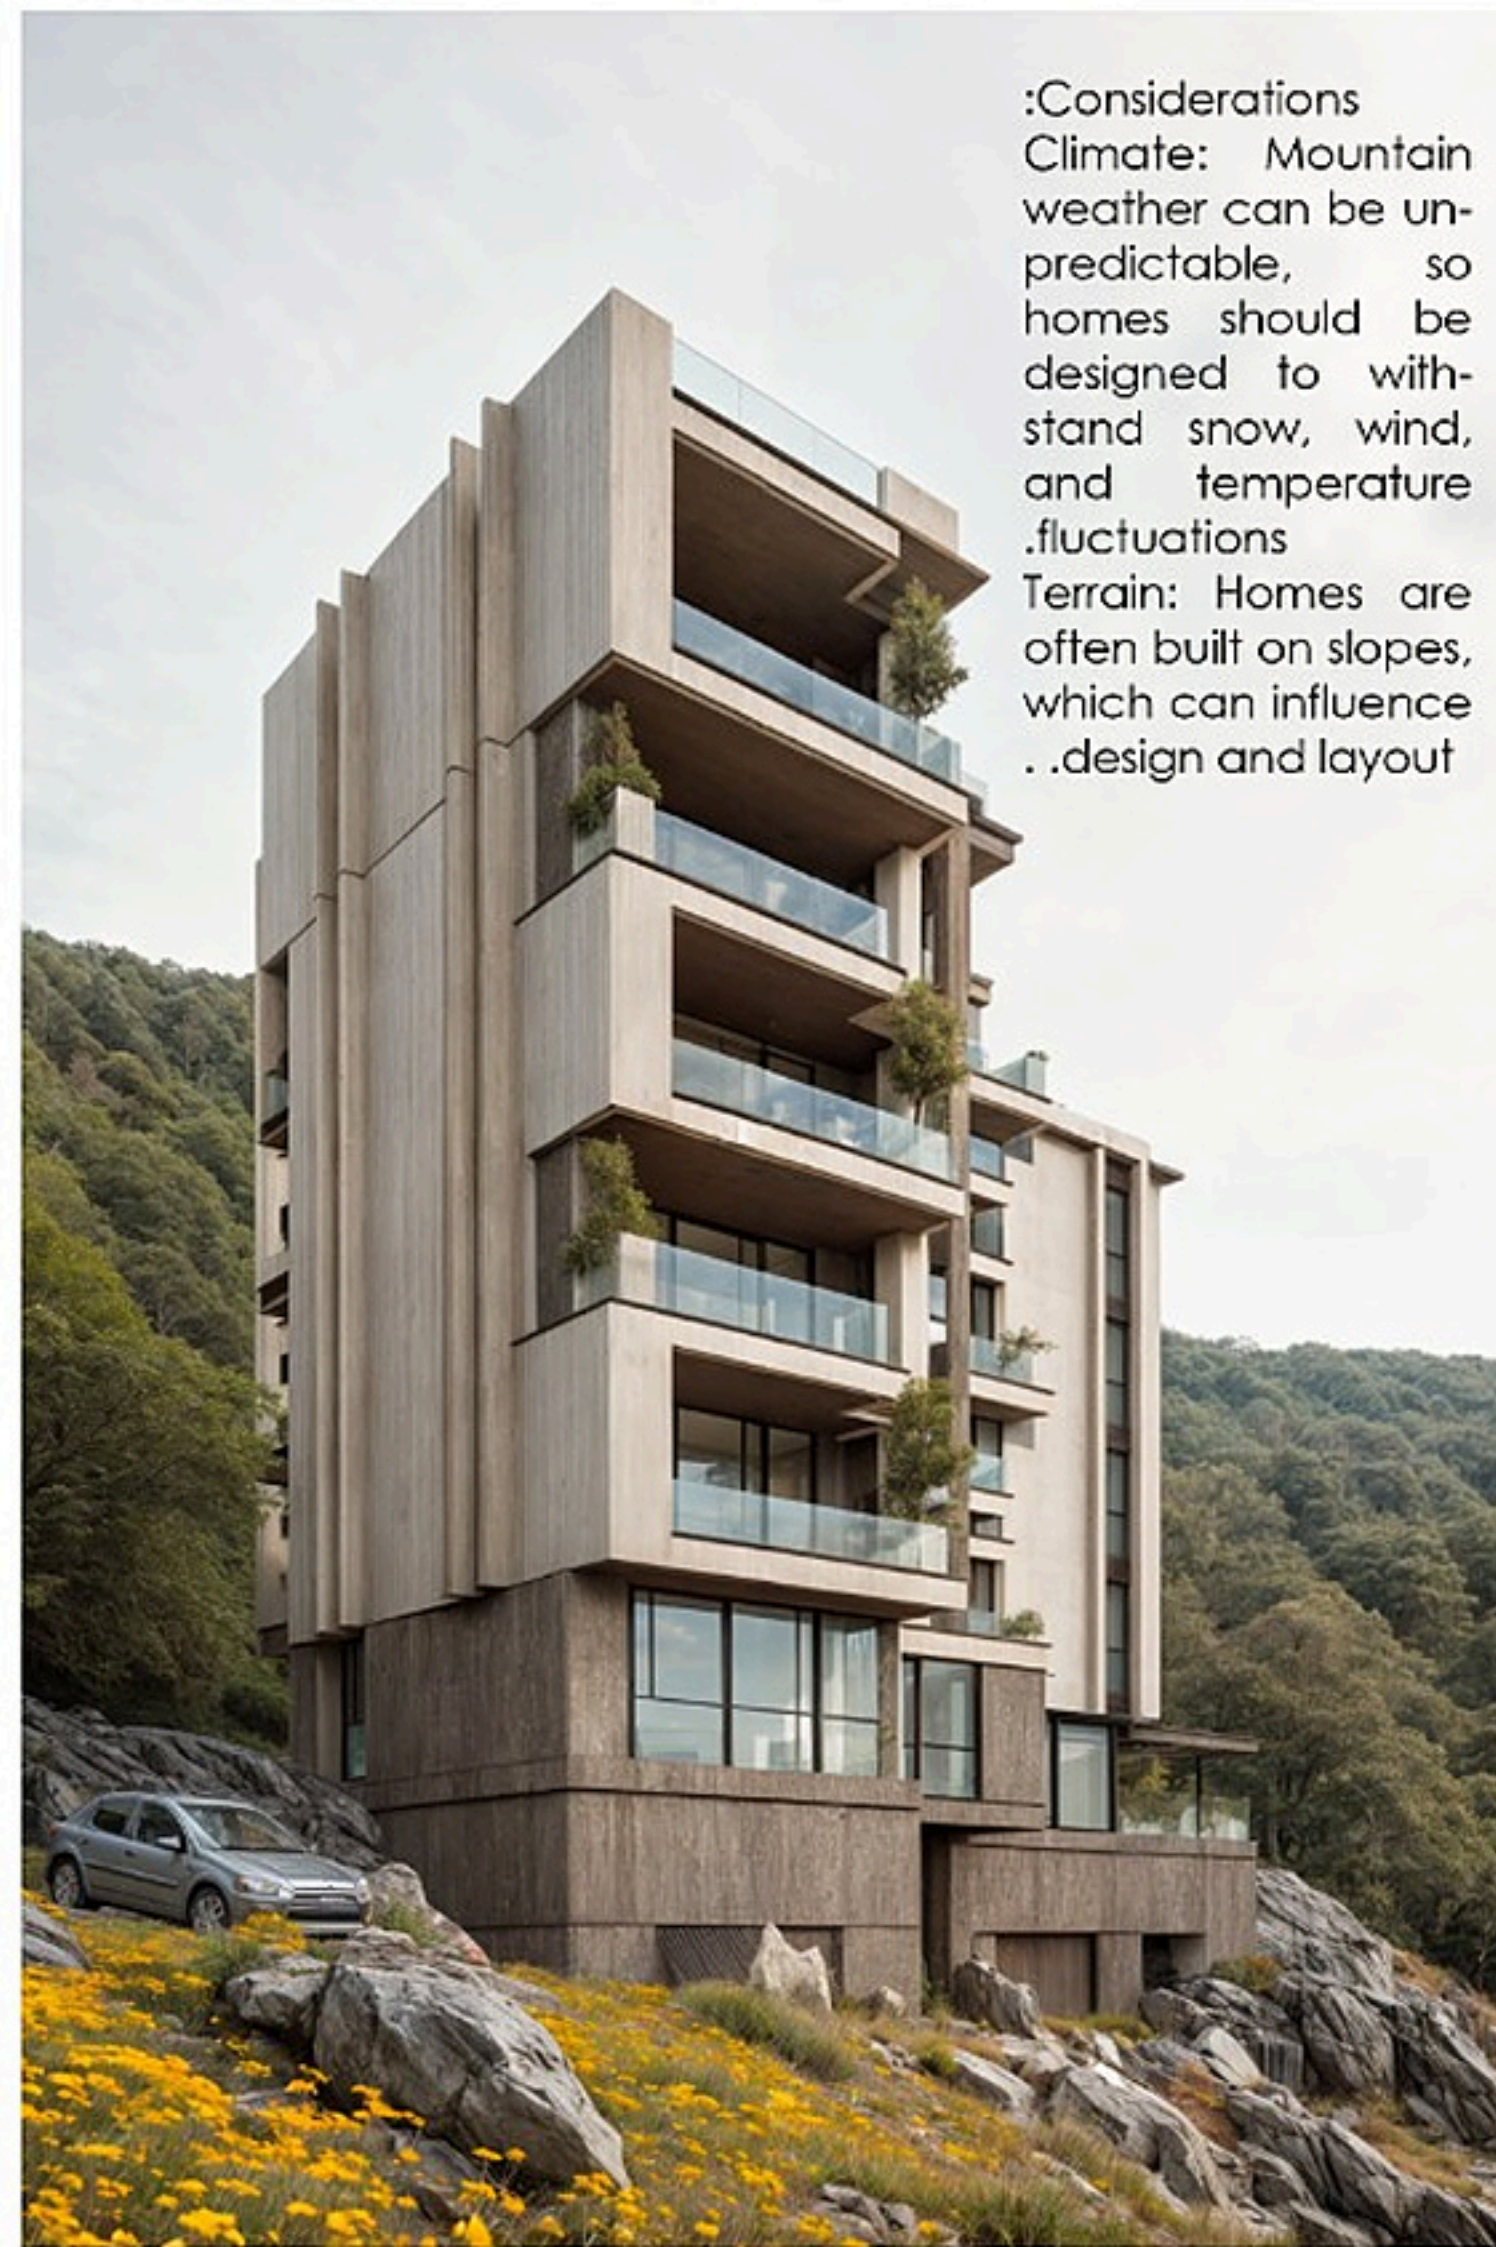

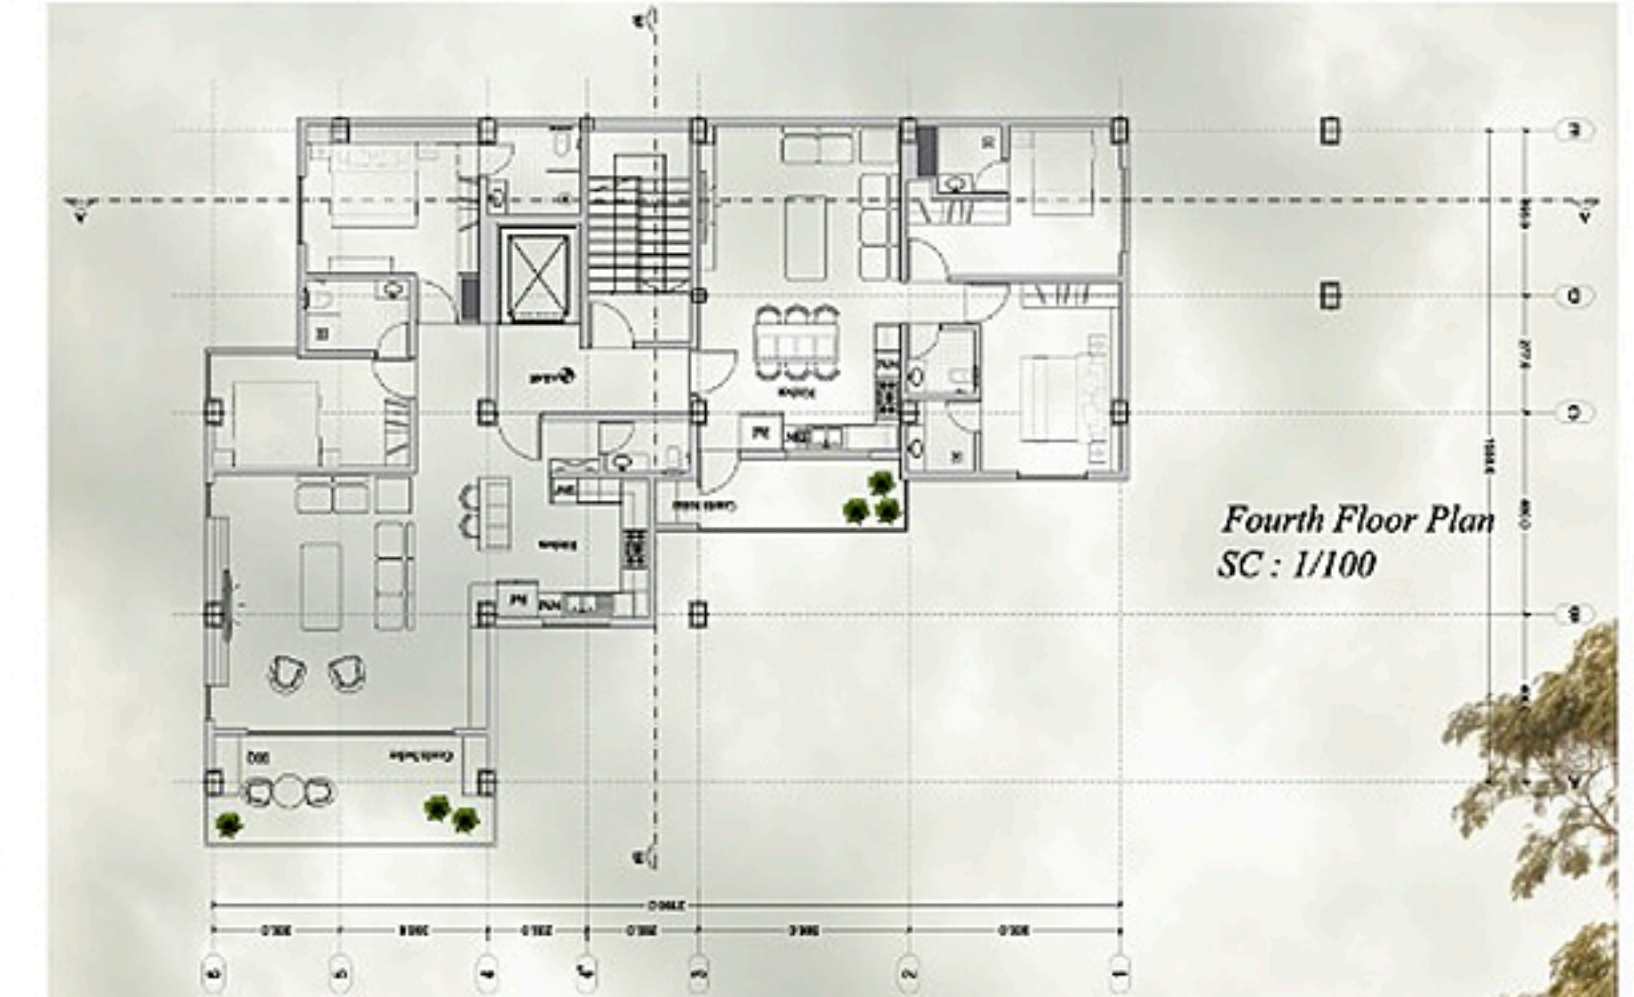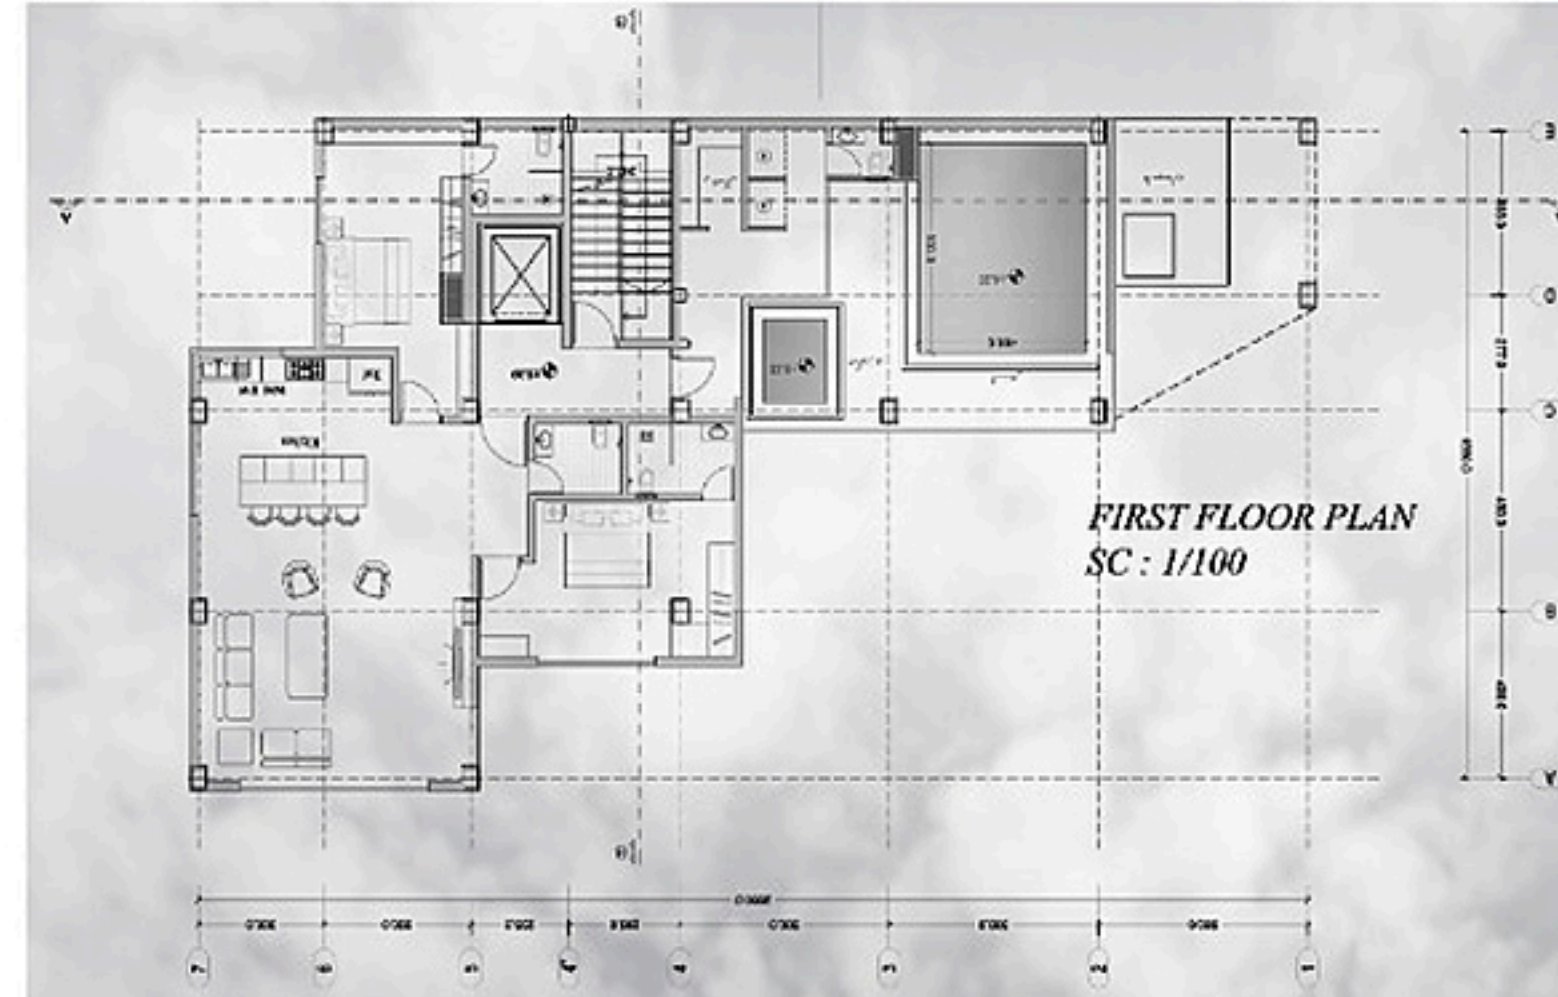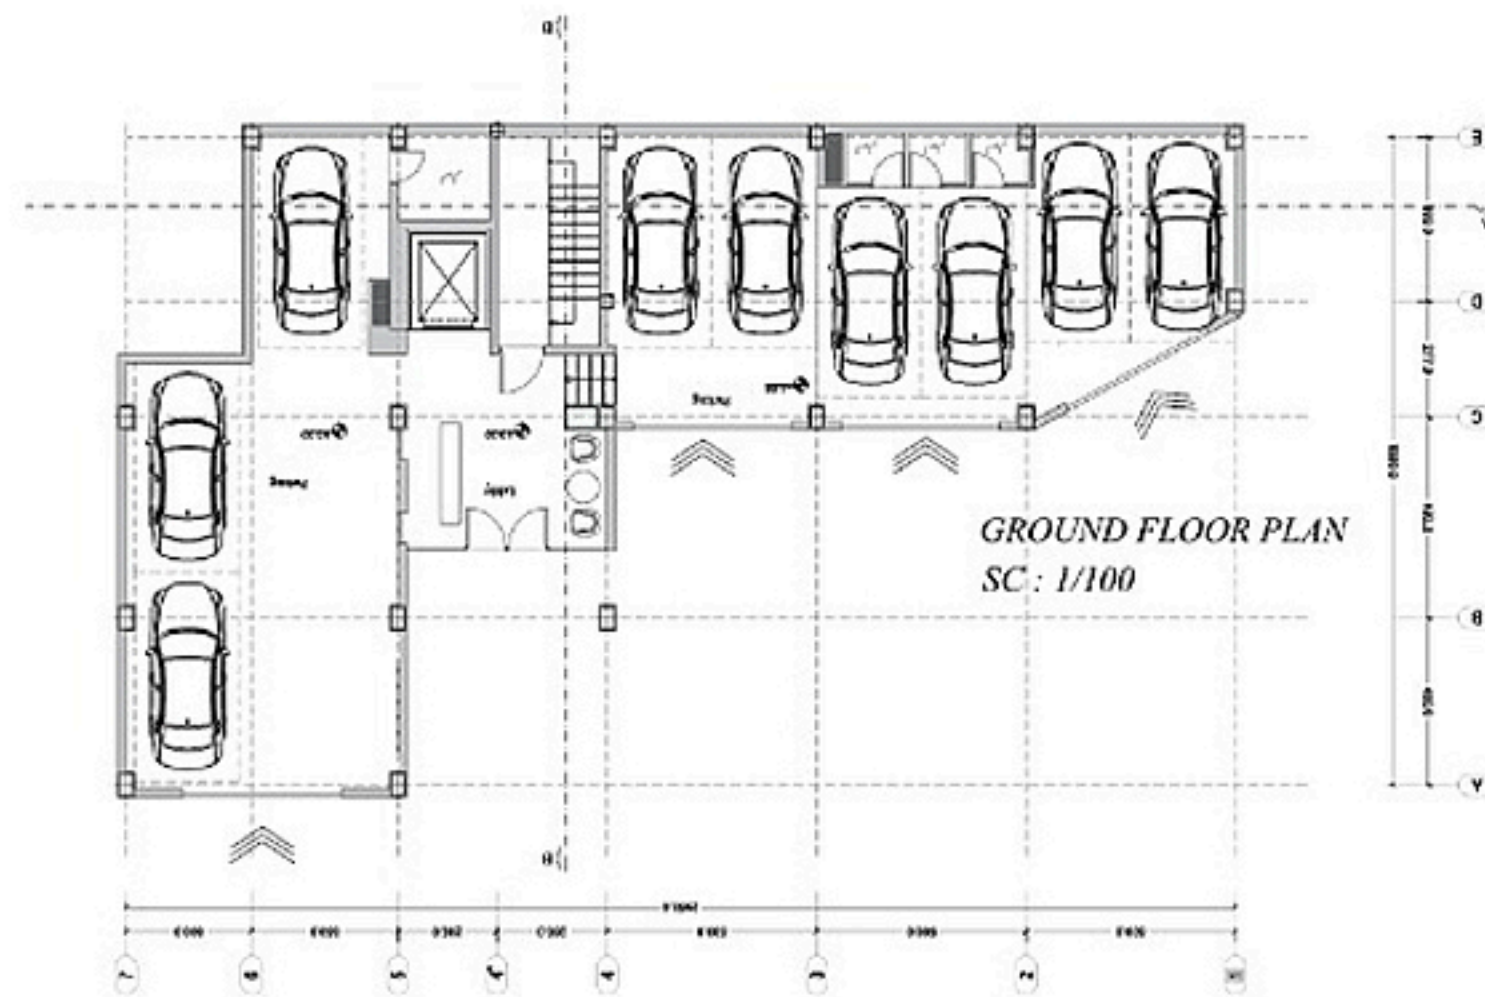

:Natural Materials

Wood and stone are prevalent, often with exposed beams and rustic details

:Large Windows

Expansive windows are a hallmark, designed to maximize views of the surrounding mountains and landscape

:Outdoor Living Spaces


Front and back porches, patios, and outdoor fireplaces are common features

:Open Floor Plans

Large, open living areas are typical, often complemented by more private bedrooms and functional spaces like mudrooms






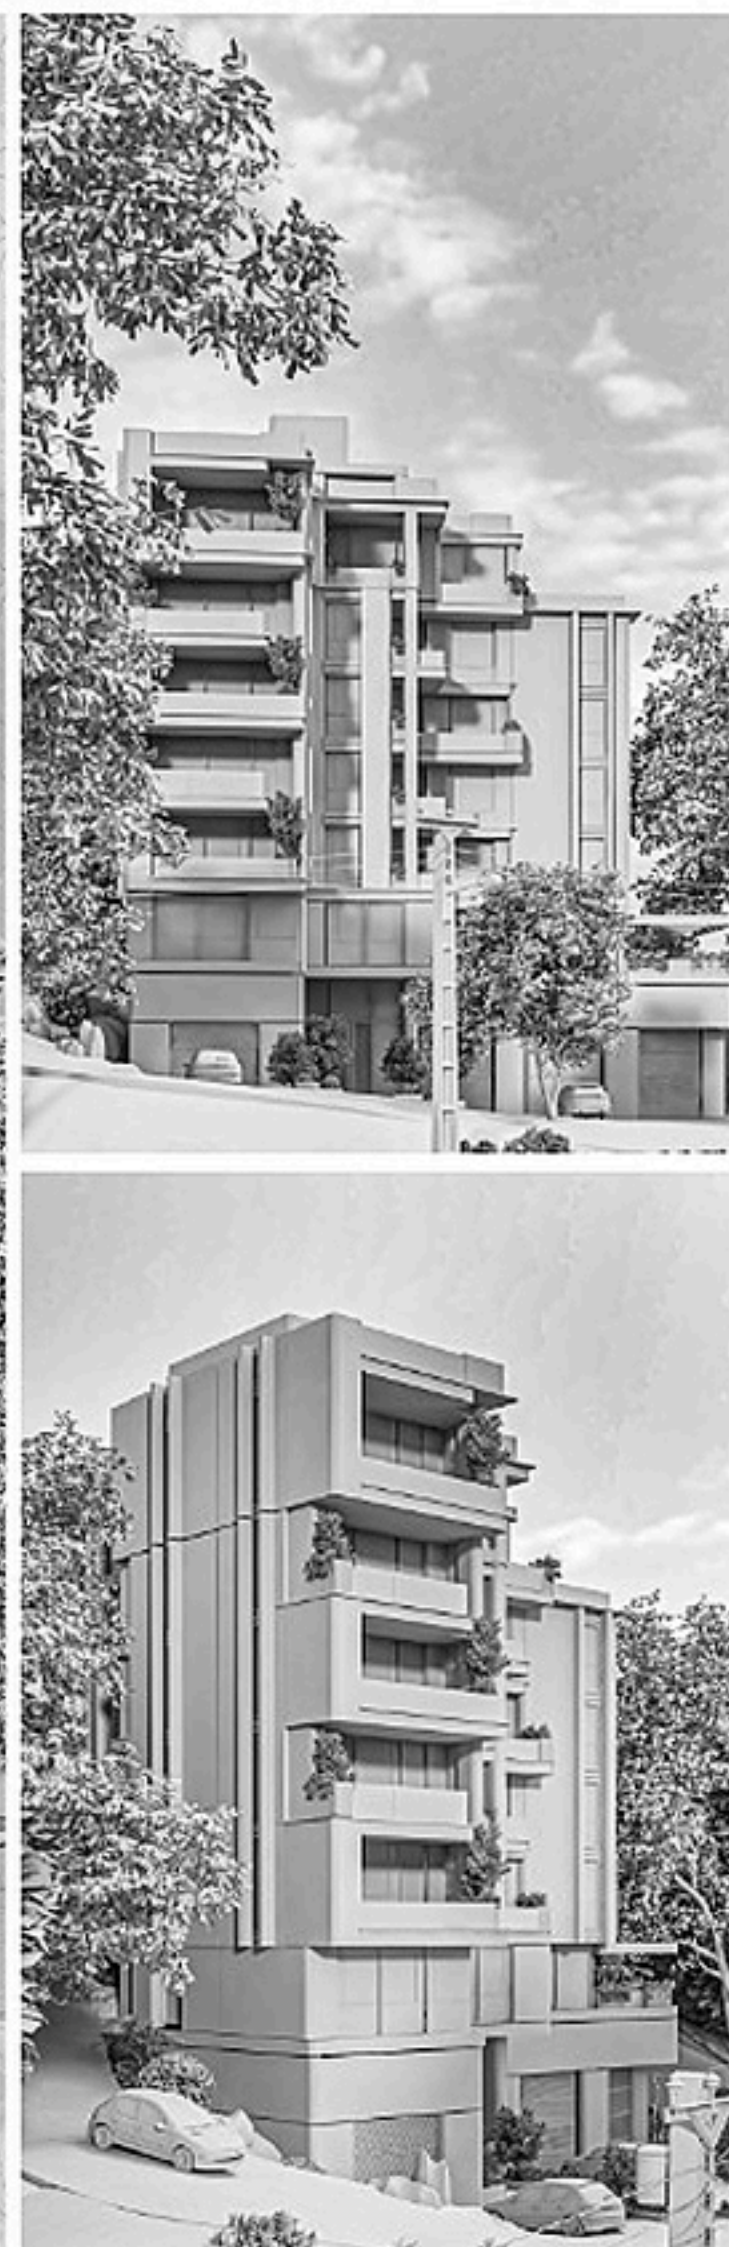

They may incorporate elements like concrete construction, designs, or "mountain modern" aesthetics that combine contemporary design with natural surroundings. Outdoor living spaces, such as covered porches and patios, are also common features, allowing residents to fully enjoy the mountain environment



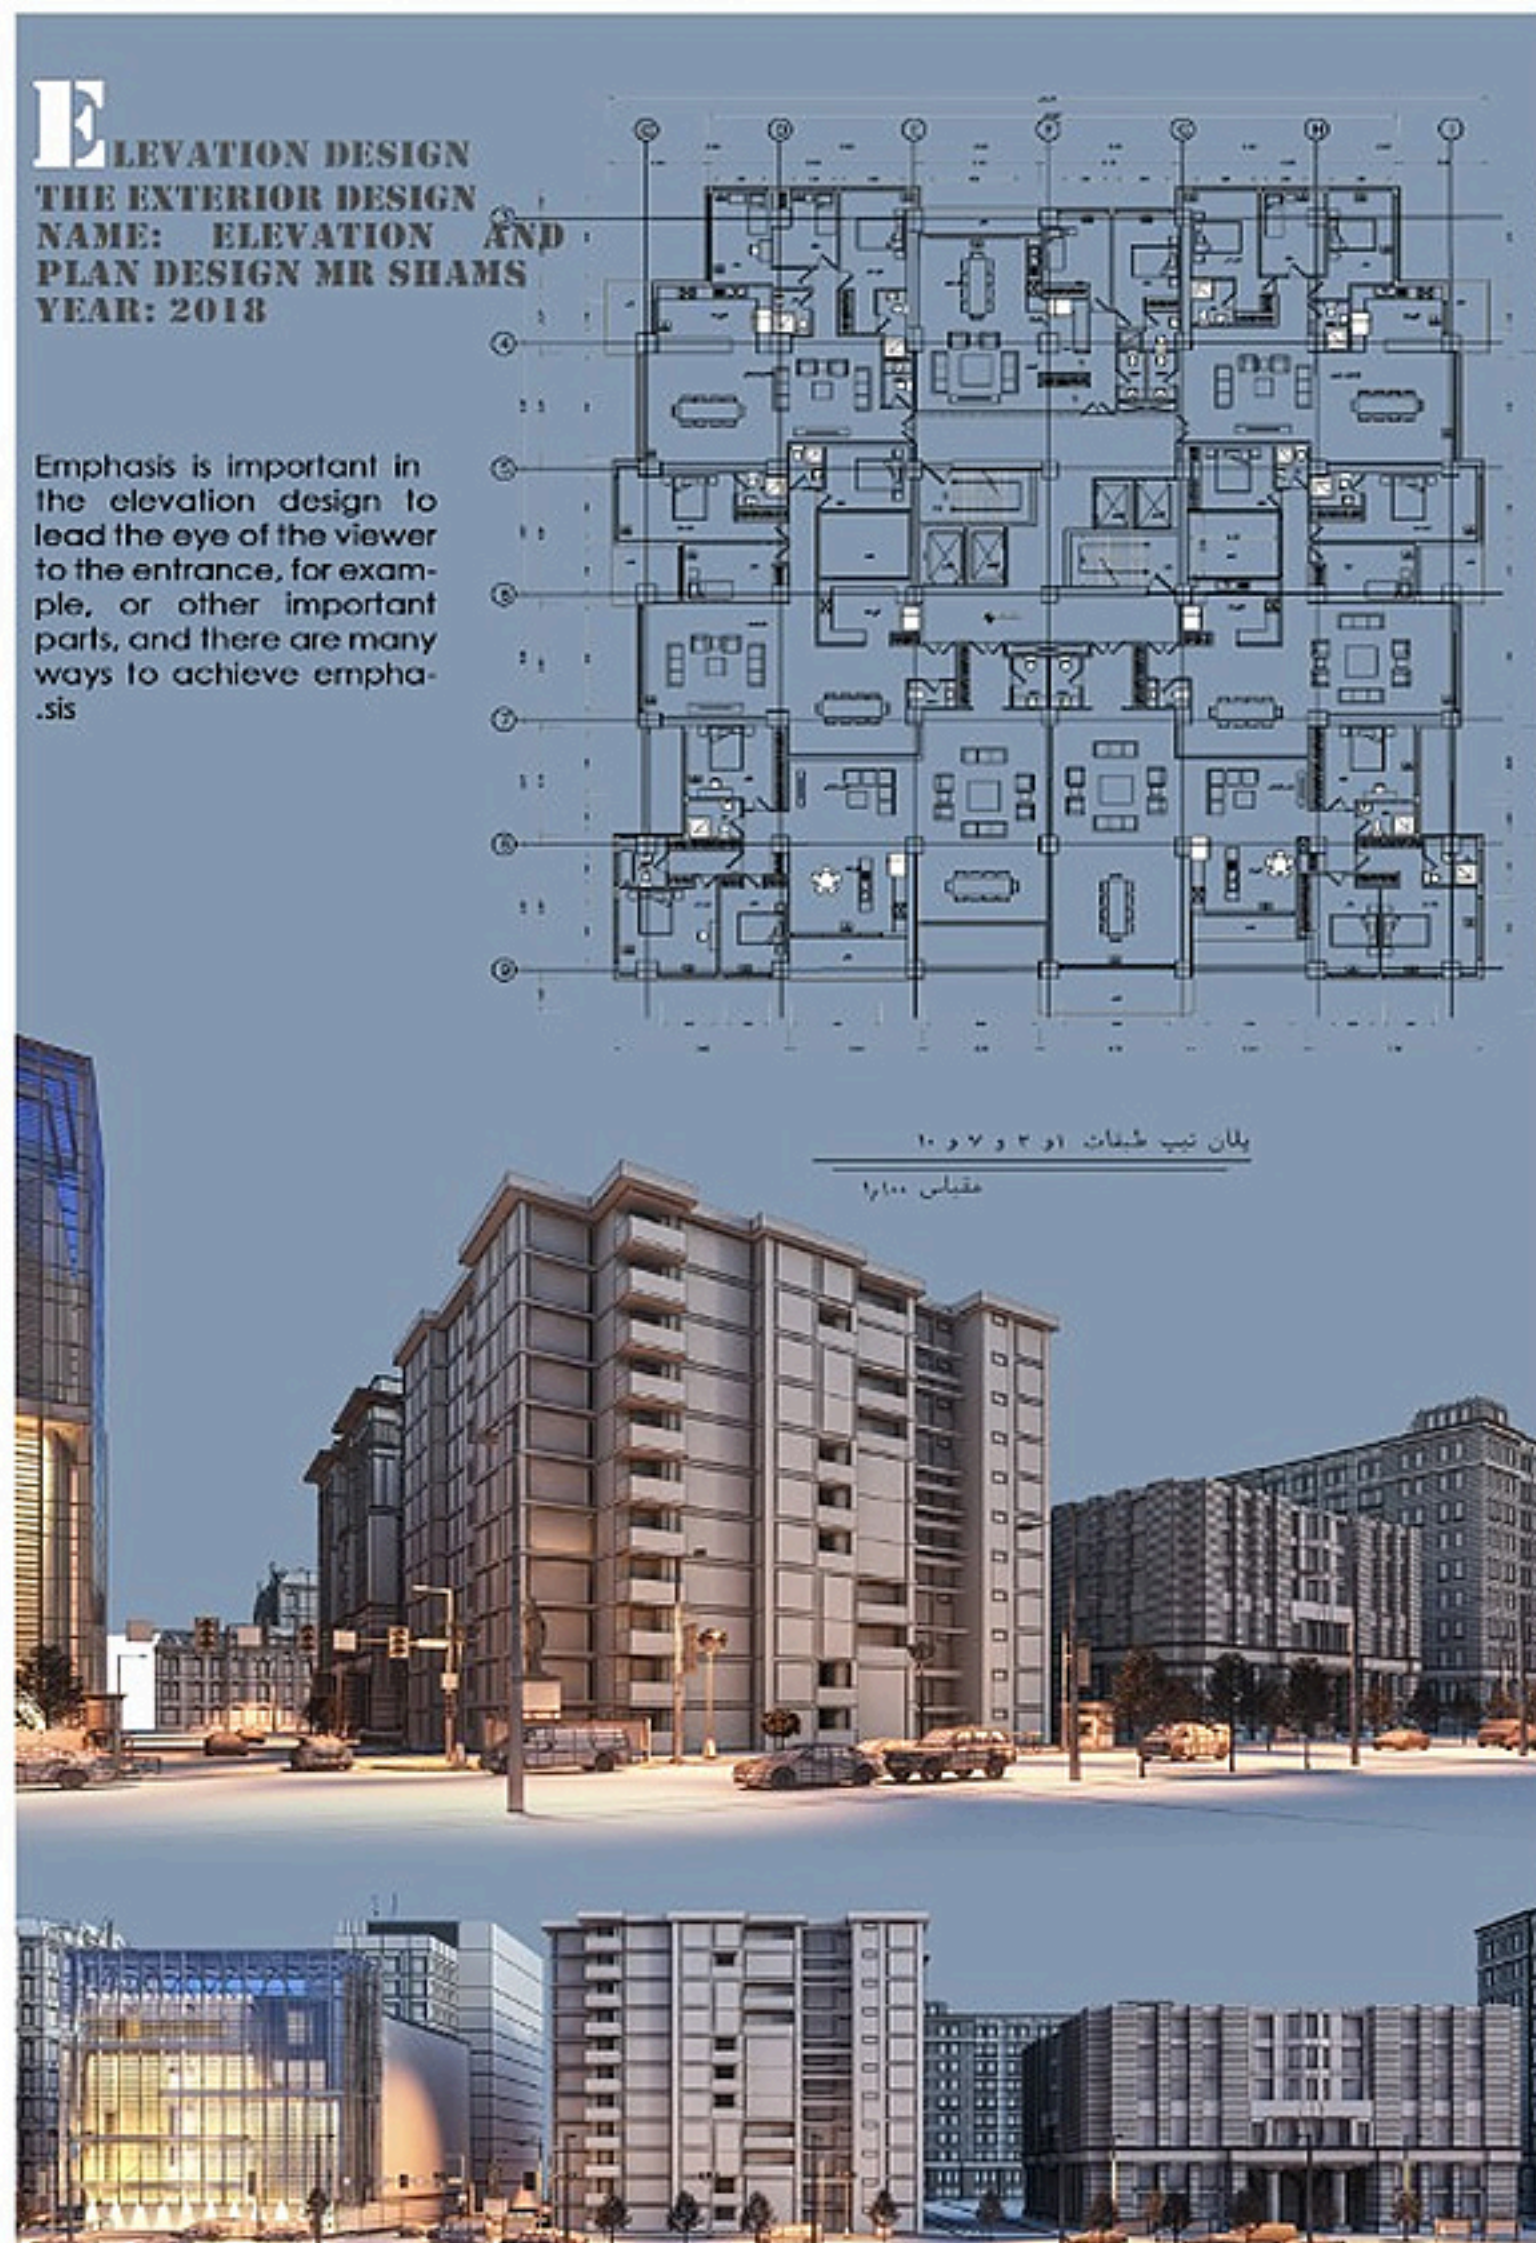

EXTERIOR DESIGN MODERN ELEVATION

THE EXTERIOR DESIGN

Proportions are vital in architecture, and naturally in elevation design. They can make or break a design. Rules were being devised since the time of ancient Greece to obtain perfect proportions, and here are some of the most commonly used proportions in design




Emphasis is important in the elevation design to lead the eye of the viewer to the entrance, for example, or other important parts, and there are many ways to achieve emphasis. Emphasis, by contrast, is one way. This contrast can be created by color or shape and texture

There is also emphasis by isolation. Isolating one element from the successive pattern of the rest make it a focal point in a way e center




Lighting is one of the most important parts of the design. The proper lighting of the building at night gives it a special effect and attracts attention. Lighting of each type of building has its own principles. Lighting modern buildings with classic buildings is completely different. The project is carried out using warm lighting colors.

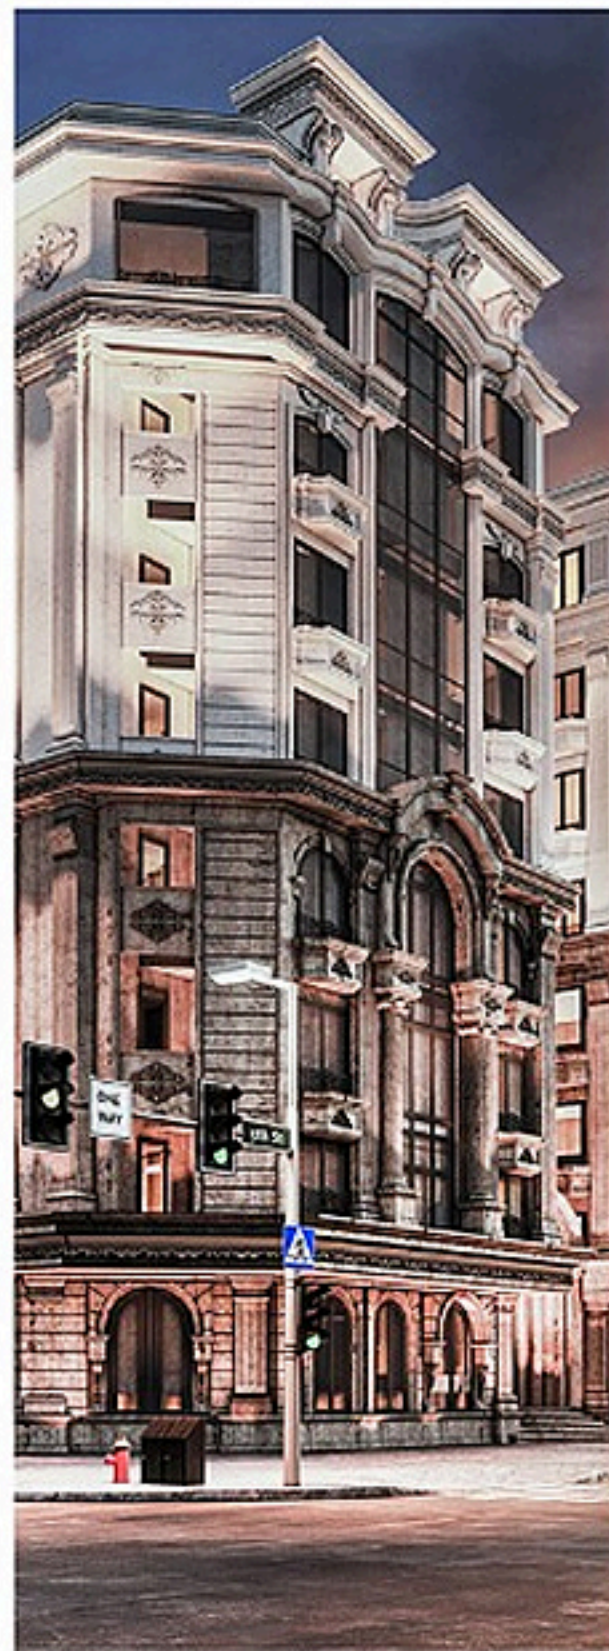

BUILDING FAÇADE DESIGN THE EXTERIOR DESIGN


The design of the building is divided into two separate sections, which are quite similar to each other and are only connected on the ground floor. The building is located at the corner of the main street, so its classic and imposing design also makes the main street look and doubles its beauty.

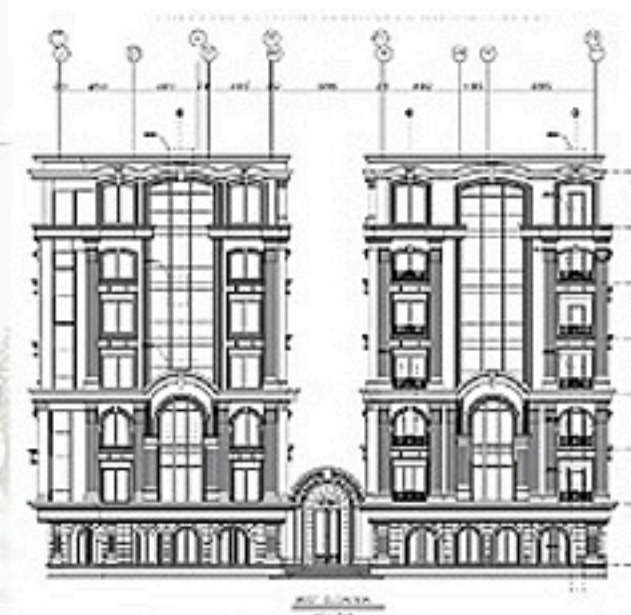

In the design of classic façade lighting, it should be avoided the embedding of light sources in vain and tailored to the type of elements and details of the lighting façade.


Using lighting with the aim of emphasizing the classical elements that show the architectural magnificence of the façade of this type of building. For example, columns, columns are symbols of height and grandeur, and the lighting of vertical elements helps to enhance the magnificence of the façade. The other is the vaults and heads, usually seen in the classic view, where the lighting of this section contributes to the luxury of this style.

Considering the use of the building and with the knowledge of its design type, we should design its lighting.

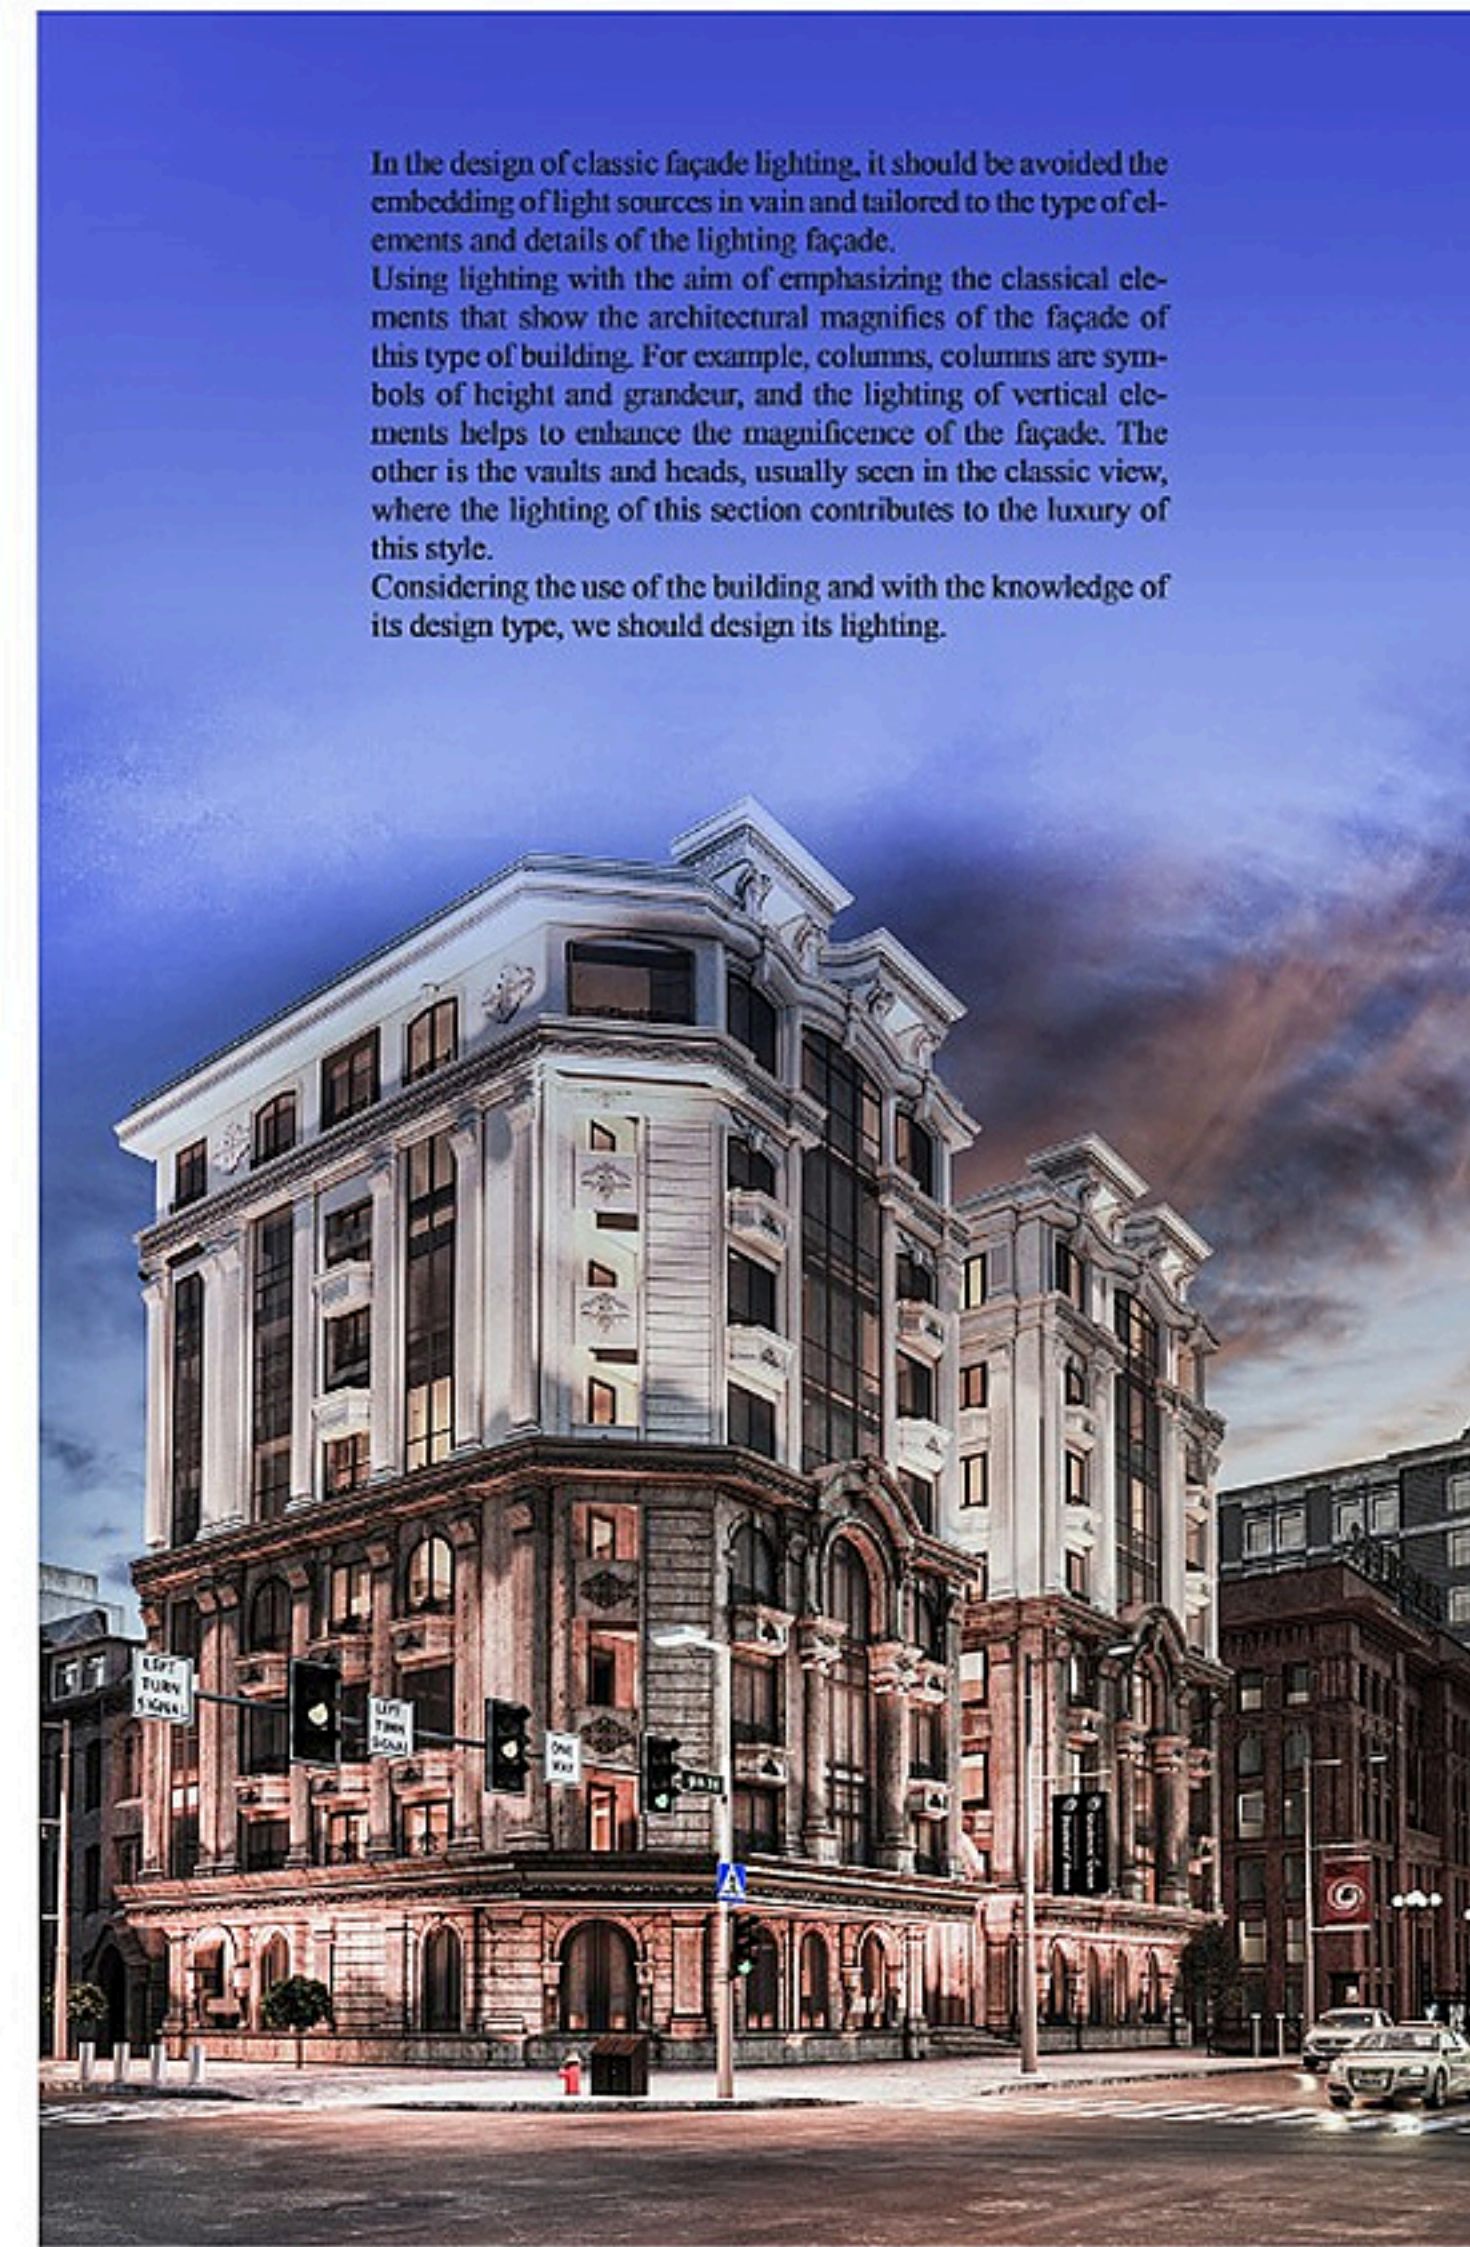



Balance is another essential factor that should be present in the design of an architectural elevation. The most obvious way to achieve balance is by symmetry. This has been done since the ancient times. However, symmetry is not the "thing" now. Contemporary architects believe in the more indirect methods.

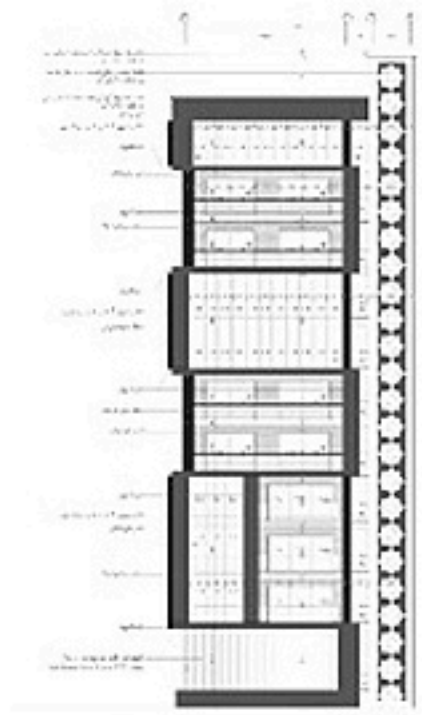

Emphasis is important in the elevation design to lead the eye of the viewer to the entrance, for example, or other important parts, and there are many ways to achieve emphasis. Emphasis, by contrast, is one way. This contrast can be created by color or shape and texture.

There is also emphasis by isolation, isolating one element from the successive pattern of the rest, make it a focal point in a way a center.



ELEVATION DESIGN


THE EXTERIOR DESIGN

NAME: ELEVATION AND

PLAN DESIGN MR SHAMS

YEAR: 2018

Emphasis is important in the elevation design to lead the eye of the viewer to the entrance, for example, or other important parts, and there are many ways to achieve emphasis.

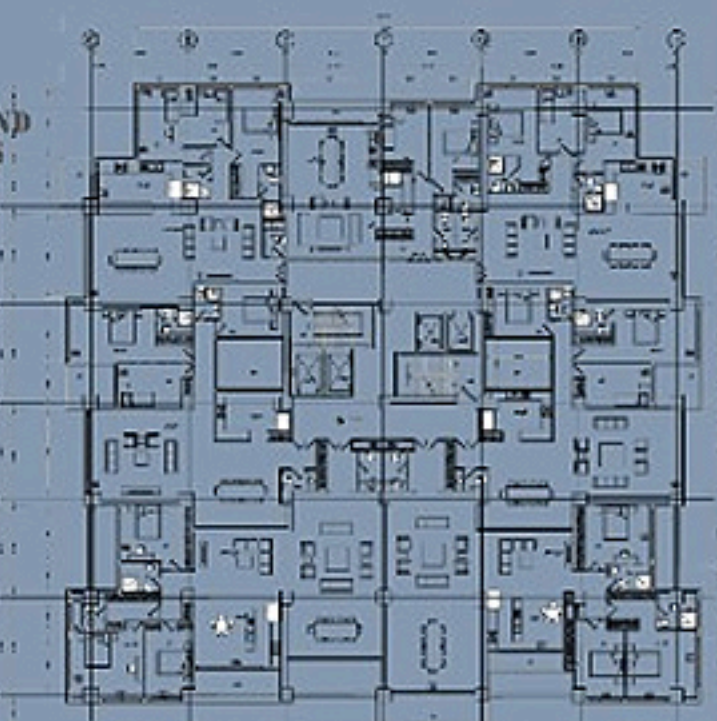


پلان طبقه اول و دوم و سوم
مشانی







While your architectural elevation needs to have unity it, also, needs variety or it will be boring. On first glance, both concepts might seem to be opposing, but in design, this is what "we call" variety within unity.



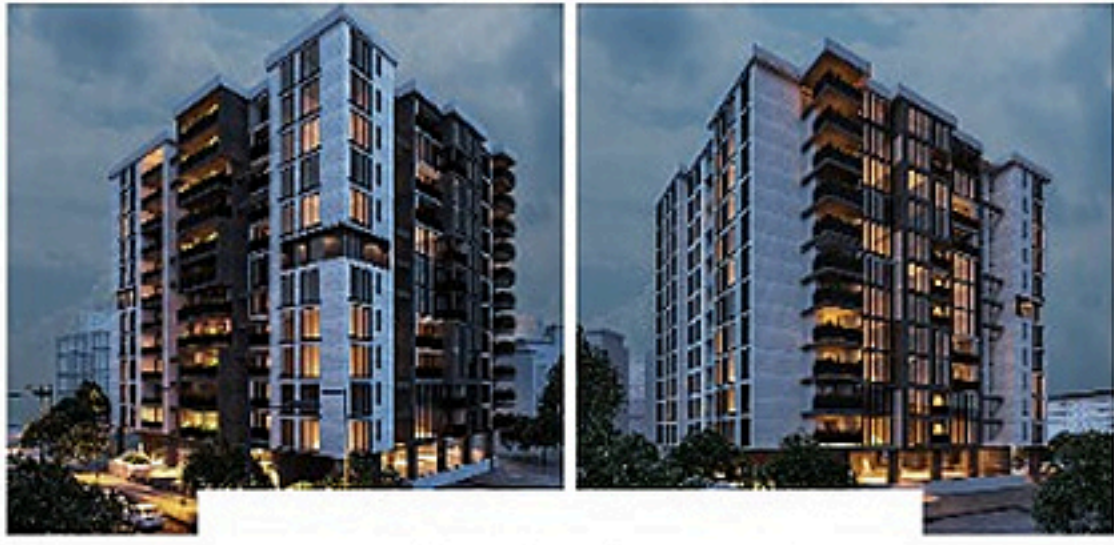


First of all, we have to be aware that architectural elevation design is like any other design in general, meaning that the basic rules and principles of design apply. While we may disagree on the word "rules" in design, but there is a set of characteristics that are always found in a successful design, whether they were respected consciously or subconsciously.

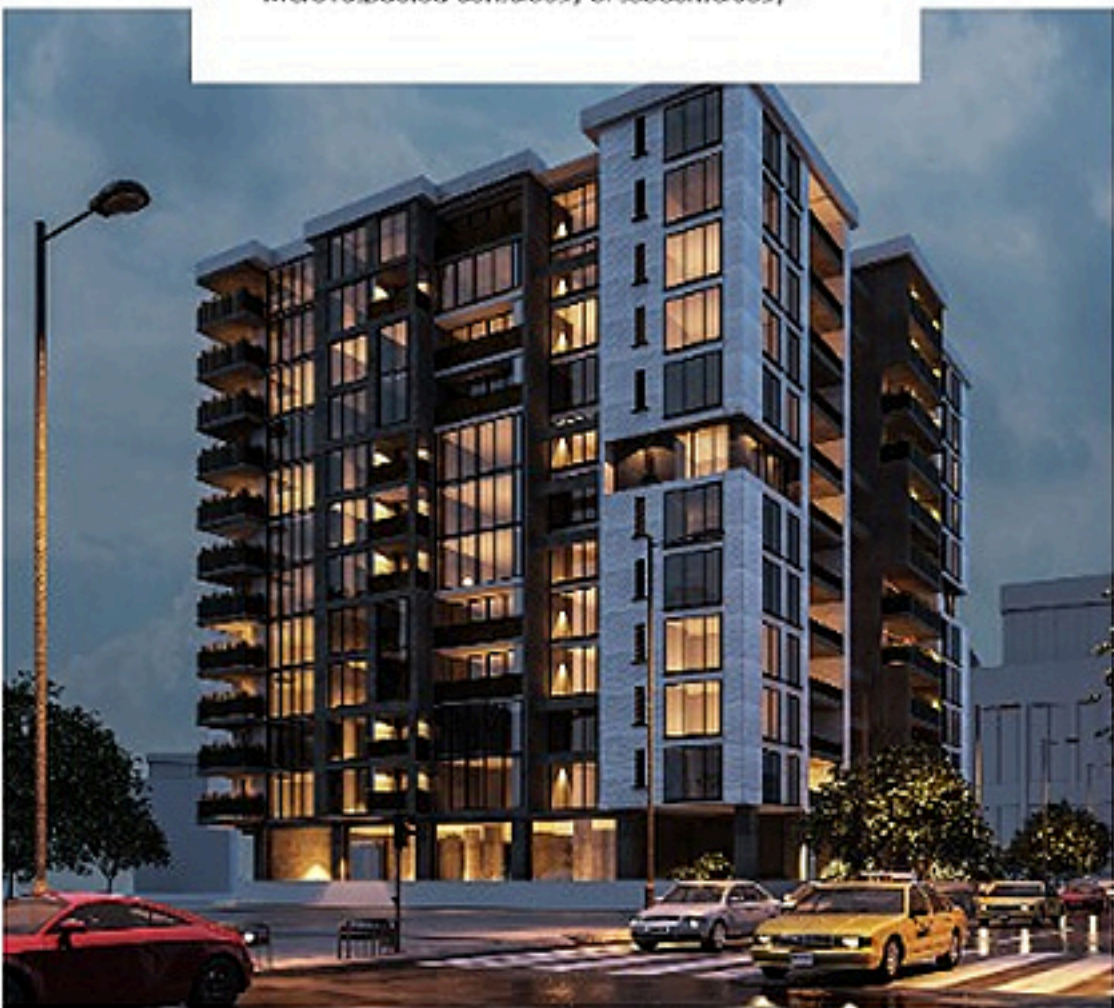

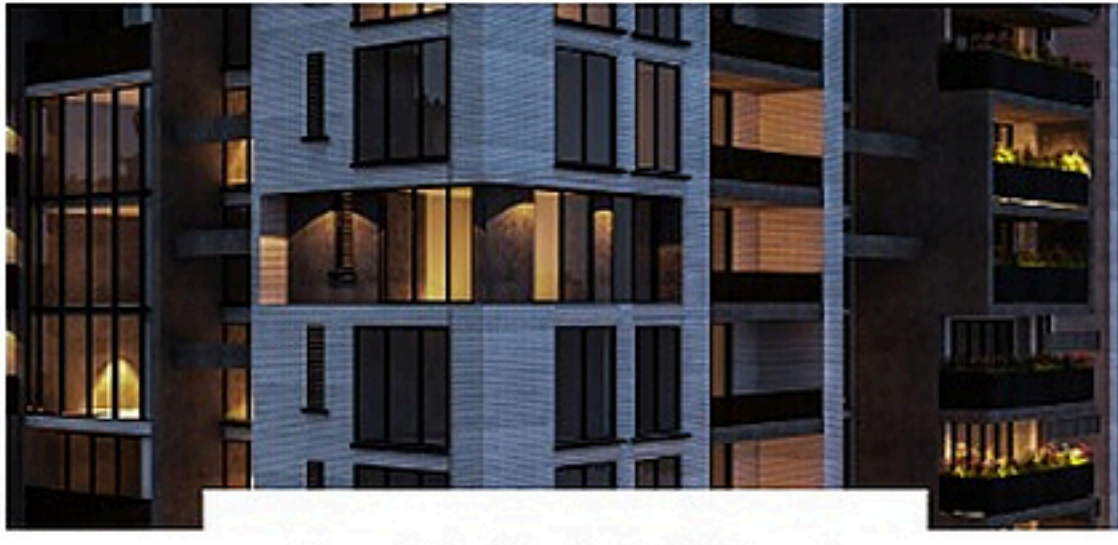

Your architectural elevation should be harmonious with a degree of unity. Unity makes the different elements and components of the elevation seem to be one, a whole instead of parts. There are different ways to achieve unity.

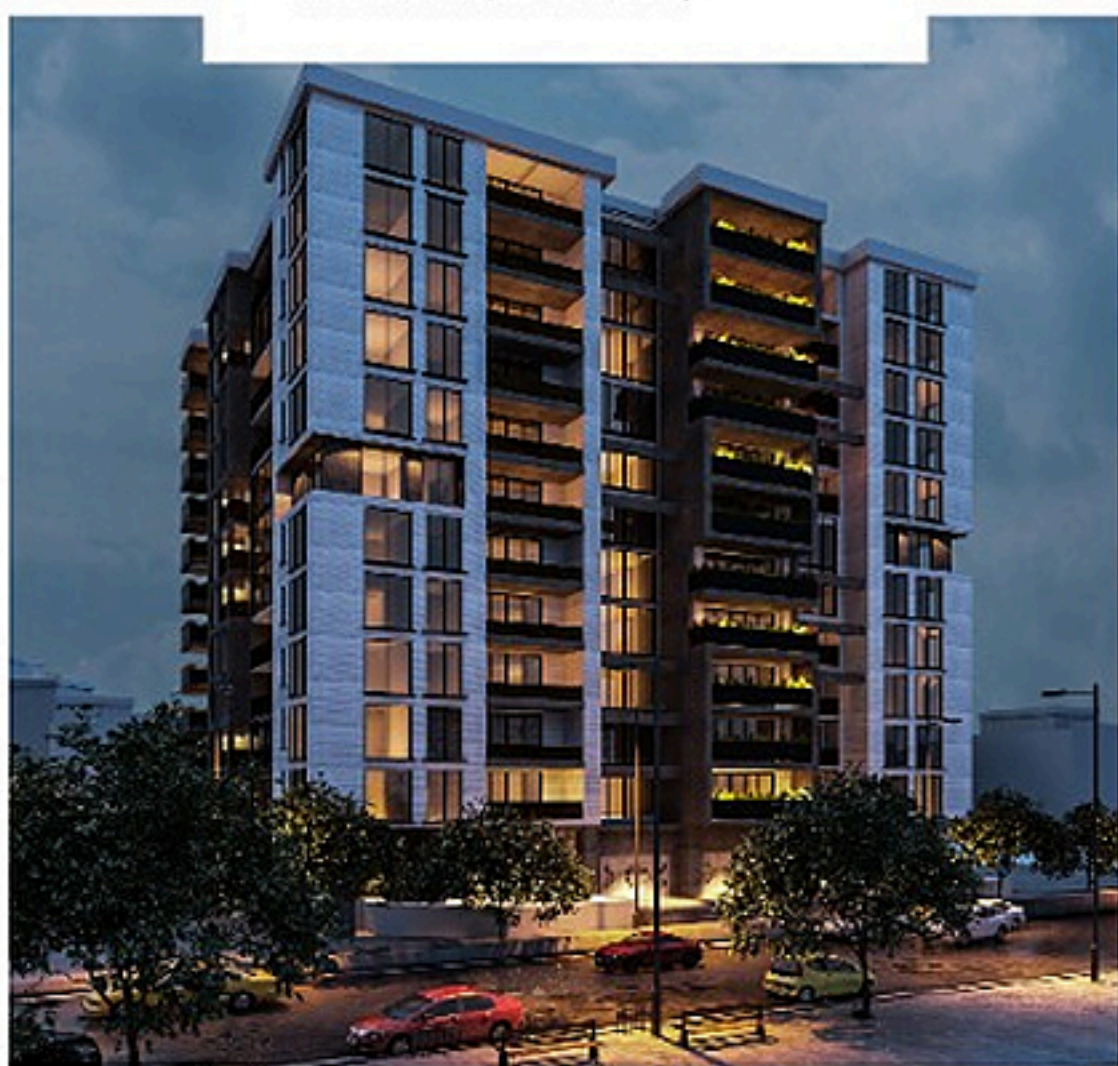



ELEVATION DESIGN

We are all well informed of the importance of executive data and know that the more these details are in the works, the more professional and mature the work seems, but before we look at how the views and the executable data should be implemented, we need to have the right materials, the condition for achieving a good view is to know what materials are most beautiful together and harmony. Create more in the view.




EXTERIOR DESIGN MODERN ELEVATION
THE EXTERIOR DESIGN

Proportions are vital in architecture, and naturally in elevation design. They can make or break a design. Rules were being devised since the time of ancient Greece to obtain perfect proportions, and here are some of the most commonly used proportions in design





Balance is another essential factor that should be present in the design of an architectural elevation. The most obvious way to achieve balance is by symmetry. This how it has been done since the ancient times. However, symmetry is not the "thing" now. Contemporary architects believe in the more indirect methods

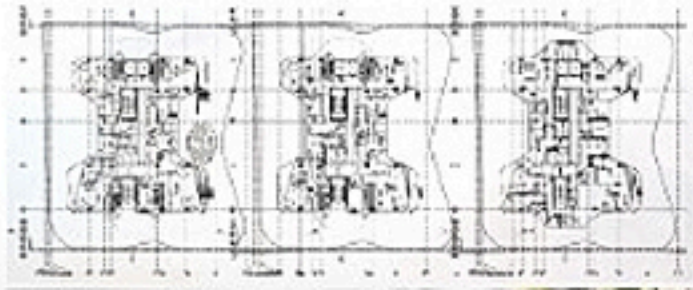

CLASSIC VILLA DESIGN
THE EXTERIOR DESIGN


In classical architecture, colors are limited because only warm colors such as brown, gold, bronze, ... are selected. The most important point that should be observed in choosing the color of such buildings is the use of one to two colors, not more. Now the classic façade is run by various builders and architects for different buildings.

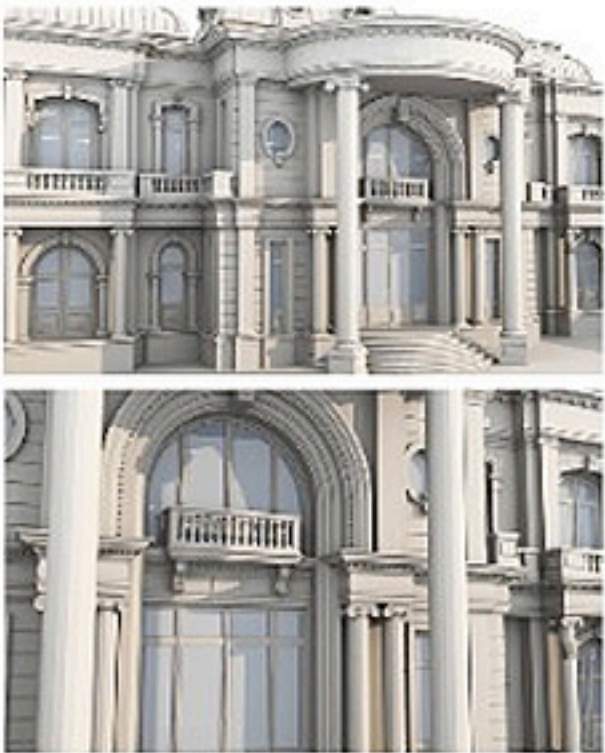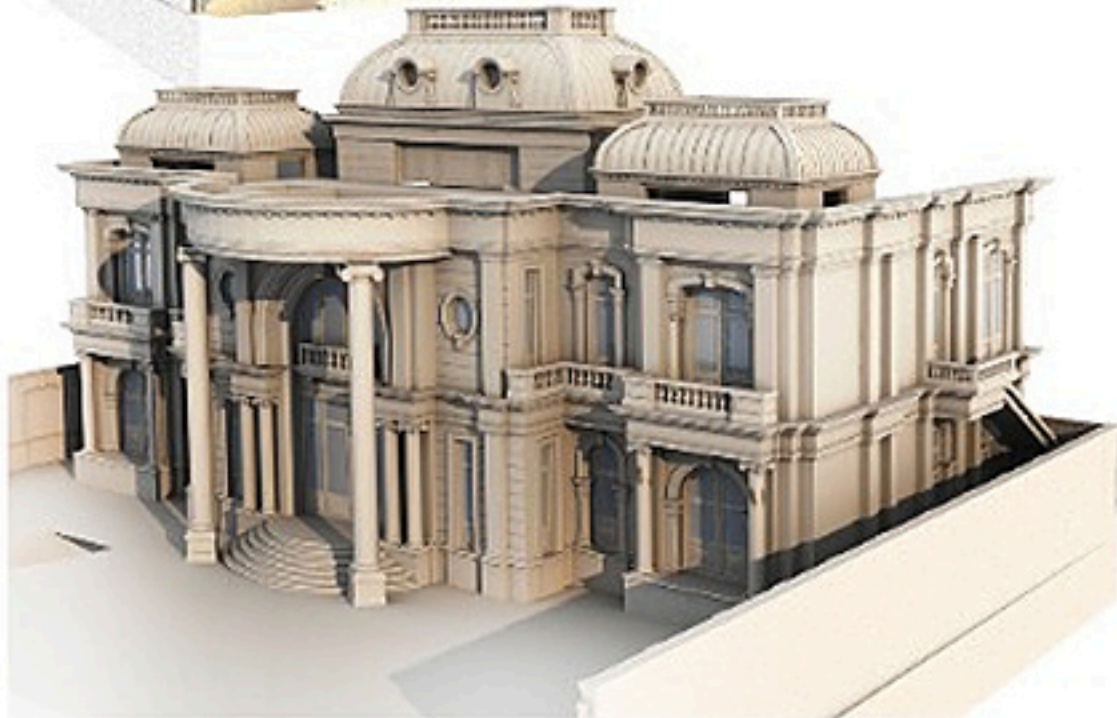

The main and basic color of this façade design should be white, because the stones used to make this type of façade are often bright. We should add that in order to implement this façade model, there is a need to use high-quality stones that can also be cut.

- Filled columns should not be used and columns with circular sections should be used.

Along with other columns, small and decorative columns were also used. Use the heads of columns that have ancient Roman design. Use large-sized arches on which prominent and delicate roles are cared for. Use different types of window frames, inscriptions, pastons, crests, etc.

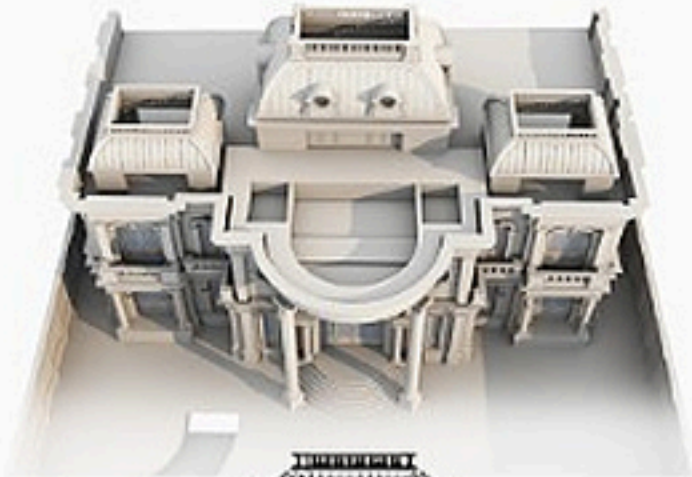

Beautiful glass doors and unique façade are the most important positive features of this material. Because of transparency, it helps to disseminate natural light in the lobby environment of the building. Also, to create a suitable insulation, the door can be made with double glass panels (two layers).



SOHEIL MASTI

BIM Director & Computational Architect

BIMCO Studio Barcelona • Spain & International

EXECUTIVE ROLES & PRACTICE SPECIALIZATION:

- Strategic BIM Implementation & Information Architecture
- Multi-discipline Clash Detection & LOD 350 Coordination
- Parametric Façade Engineering & Environmental Optimization
- Automated Quantities, Cost Modeling & Fabrication Schedules
- Executive Supervision & Construction Quality Assurance
- International Project Delivery across Spain, EU & Middle East

SIAVASH PAZOOKI

Senior Architectural Designer & High-End Visualizer

M.Arch & B.Arch • BIMCO Studio Barcelona Partner

EXECUTIVE ROLES & PRACTICE SPECIALIZATION:

- Lead Architectural Concept Designer & Spatial Formulator
- Advanced 3D Photorealistic CGI & Atmospheric Visualizations
- Complex Elevation Tectonics, Louver Systems & Material Studies
- Executive Floor Plans, Sectional Studies & Millwork Details
- Active On-Site Construction Monitoring & Build Integrity Control
- Over 8 Years Leading Signature High-End Commissions

ARCHITECTURAL VERIFICATION STANDARDS

Executive Quality Assurance & Practice Protocols

01. UNBROKEN PROJECT CONTINUITY

Every architectural commission in this monograph is presented in full chronological sequence without isolated or fragmented sheet sampling.

02. COMPUTATIONAL BIM LOD 350 INTEGRITY

All designs are backed by coordinated Building Information Models with Clash Detection, accurate material schedules, and parametric modeling.

03. VERIFIED SITE EXECUTION & SUPERVISION

Executive on-site supervisory records substantiate physical constructability, structural fidelity, and bespoke craftsmanship.

04. PERIMETER INTELLECTUAL PROPERTY

All original concepts, structural solutions, and renders are protected by international copyright under BIMCO Studio Barcelona.

05. COLLABORATIVE CLIENT ADVISORY

Direct partner access to principals Soheil Masti and Siavash Pazooki for international commissions across Spain, the EU, and the Middle East.



B I M C O

VOLUME II: RESIDENTIAL APARTMENTS & FACADES

BARCELONA, CATALONIA, SPAIN

STUDIO HEADQUARTERS

Barcelona, Catalonia, Spain

PRACTICE DIRECTORS

Soheil Masti & Siavash Pazooki

DIRECT TELEPHONE & WHATSAPP

+34 610 855 434

OFFICIAL WEB PORTAL

www.bimco.es

DIRECT INQUIRIES & COMMISSIONS

info@bimco.es

© 2026 BIMCO STUDIO BARCELONA. ALL RIGHTS RESERVED.